


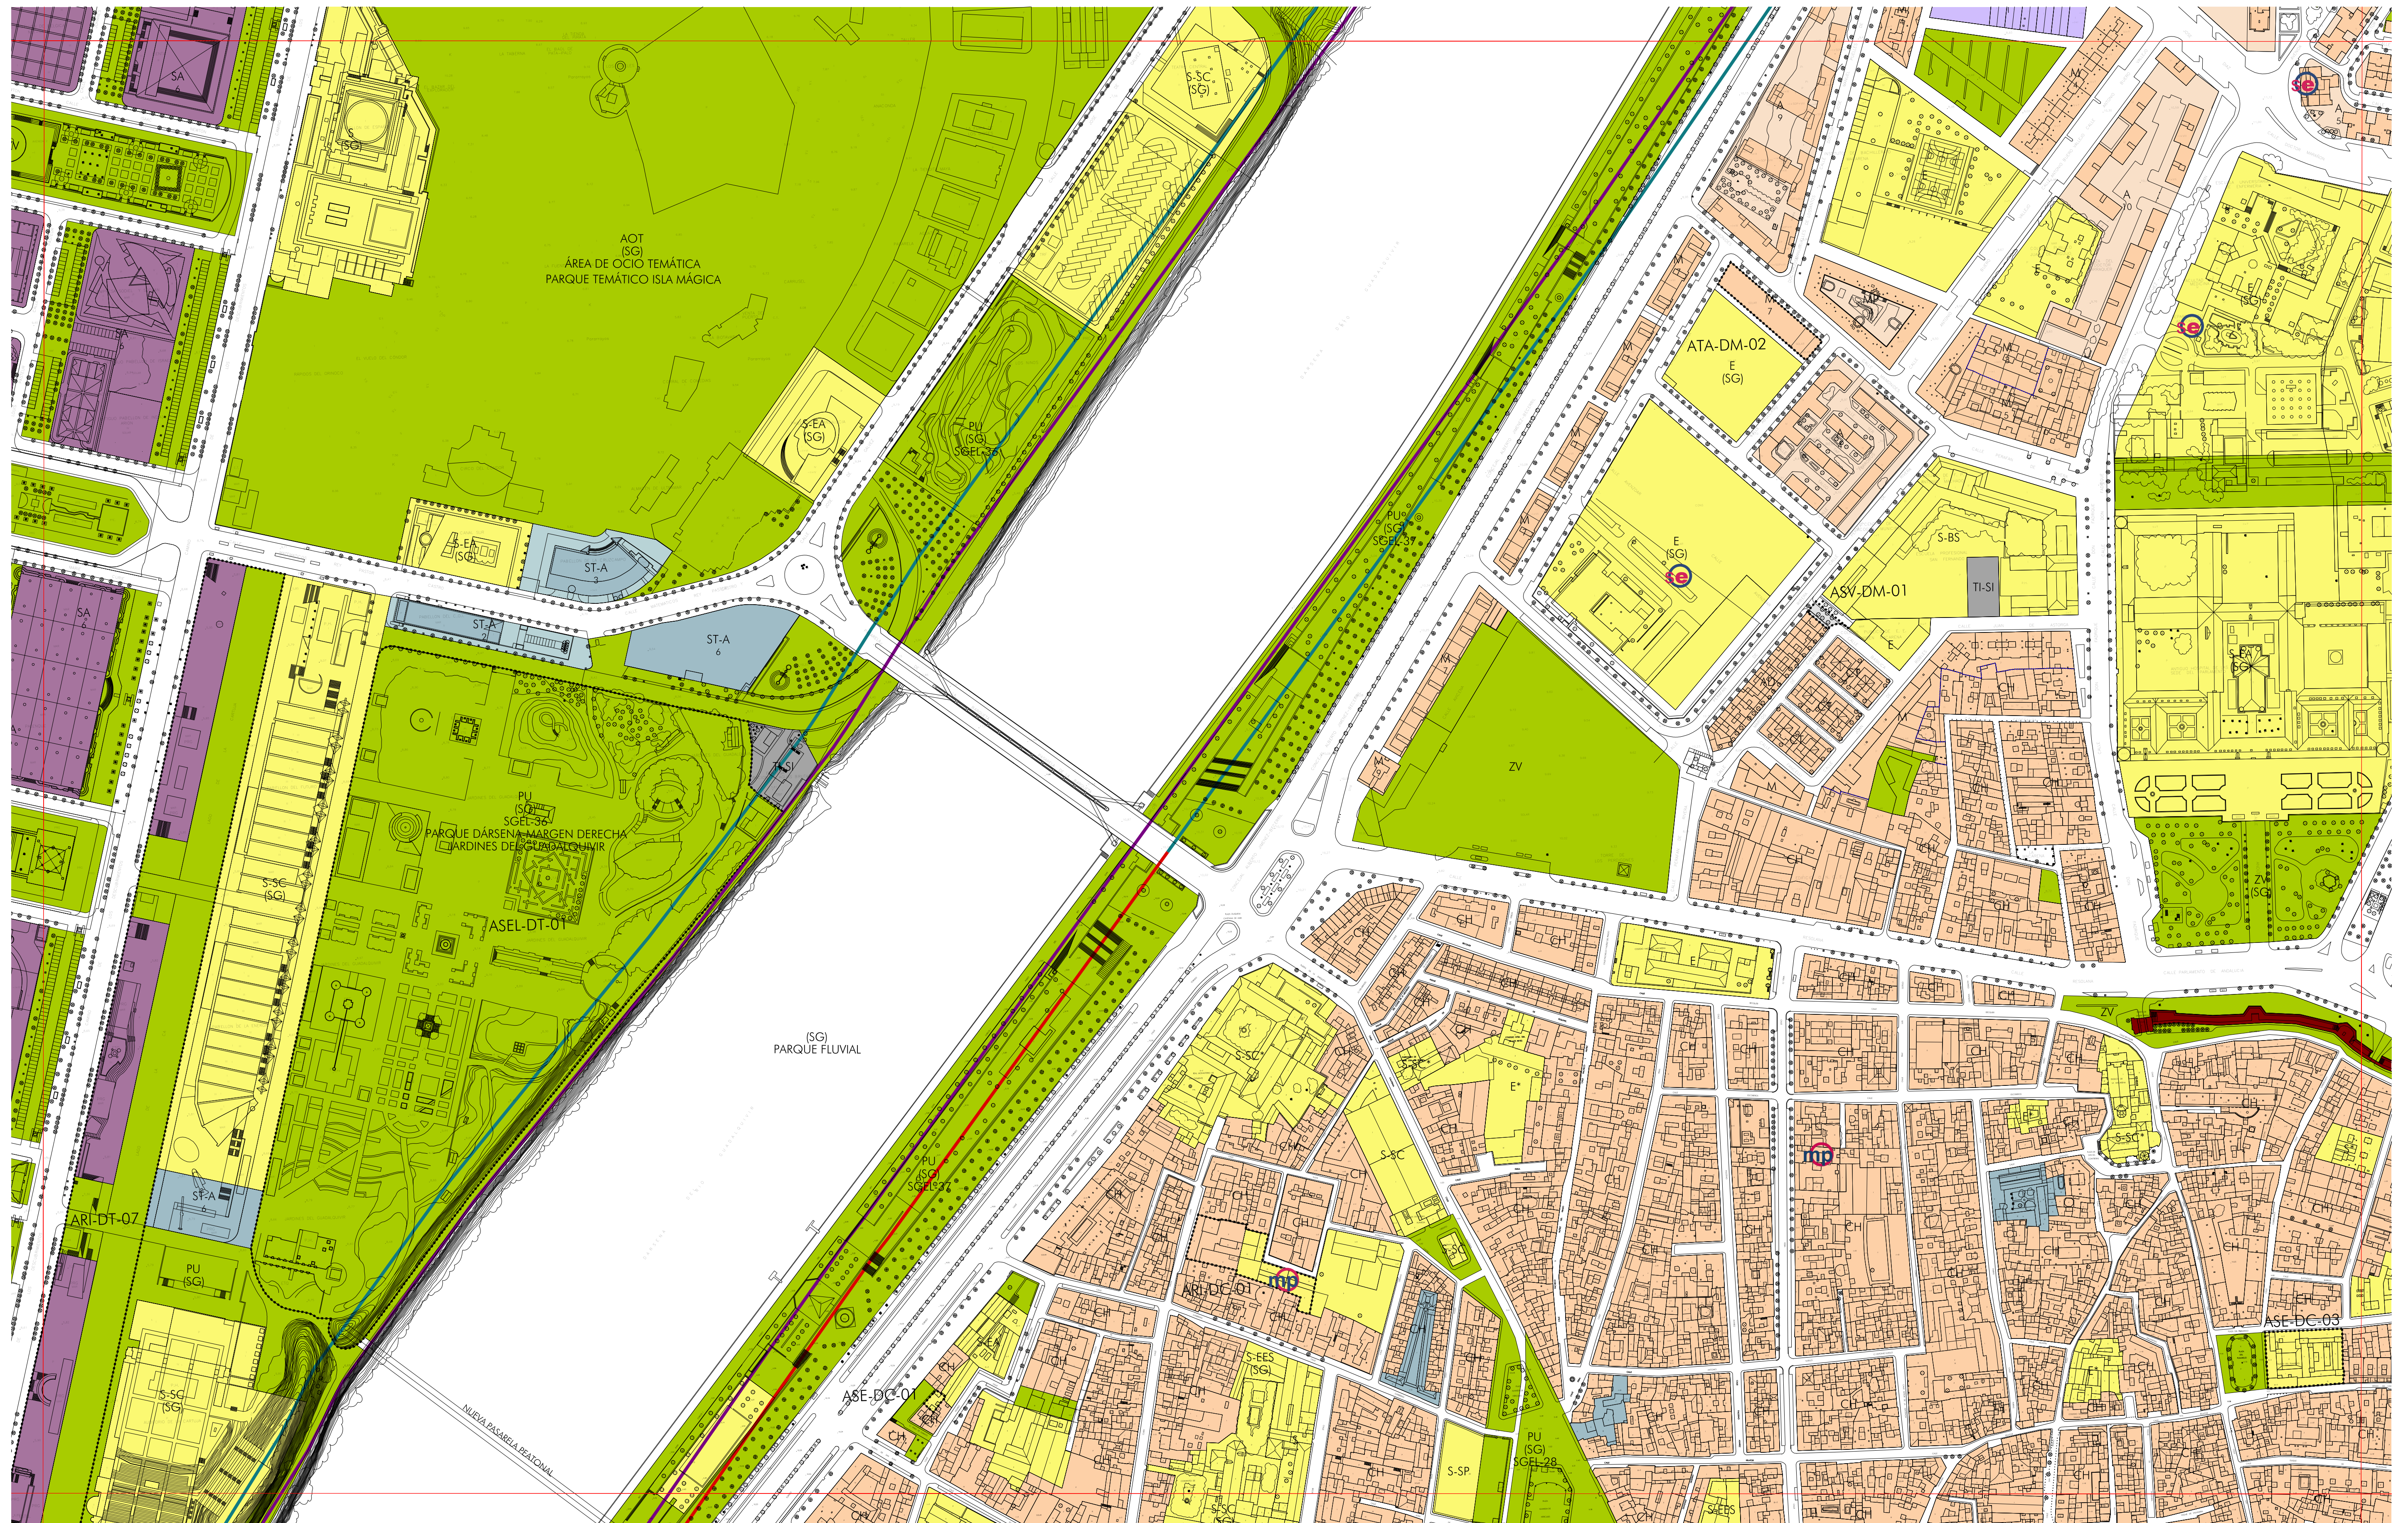

USOS GLOBALES Y PORMENORIZADOS

RESIDENCIAL



DOTACIONAL

EQUIPAMIENTOS Y SERVICIOS PÚBLICOS

E	EDUCATIVO
D	DEPORTIVO
S	SERVICIOS DE INTERÉS PÚBLICO
(*)	DE CARÁCTER PRIVADO

ESPACIOS LIBRES

PM	PARQUE METROPOLITANO
PU	PARQUE URBANO
ZV	ZONAS VERDES

TRANSPORTES E INFRAESTRUCTURAS BÁSICAS		TI-F FERROVIARIO
■	TI-SI SERVICIOS	TI-P PUERTO
	INFRAESTRUCTURALES	TI-AP AEROPUERTO
■	TI-CTM CENTRO DE TRANSPORTE	TI-HP HELIPUERTO
	DE MERCANCÍAS	TI-IT INTERCAMBIO

VIARIO PROPUESTO	ESPACIO LIBRE ASOCIADO AL VIARIO

- S-S
- S-BS
- S-EA
- S-SC
- S-SP
- S-EES

- FERROVIARIO
- PUERTO
- AEROPUERTO
- HELIPUERTO
- INTERCAMBIAD

DE TRANSPOR
L VIARIO

ZONAS DE ORDENANZAS DEL SUELO URBANO

CH	CENTRO HISTÓRICO
M	EDIFICACIÓN EN MANZANA
MP	EDIFICACIÓN EN MANZANA CON ALINEACIÓN INTERIOR OBLIGATORIA O MÁXIMA
A	EDIFICACIÓN ABIERTA
SJ	SUBURBANA
CB	CIUDAD JARDÍN
AD	UNIFAMILIAR ADOSADA
UA	UNIFAMILIAR AISLADA Y/O AGRUPIADA
CT	CONSERVACIÓN TIPOLOGICA
IS	INDUSTRIA SINGULAR
IA	INDUSTRIA EN EDIFICACIÓN ABIERTA
IC	INDUSTRIA EN EDIFICACIÓN COMPACTA
SA	SERVICIOS AVANZADOS
ST-A	SERVICIOS TERCIARIOS EN EDIFICACIÓN ABIERTA
ST-C	SERVICIOS TERCIARIOS EN EDIFICACIÓN COMPACTA

CLASIFICACIÓN Y CATEGORÍAS DE SUELO. DETERMINACIONES COMPLEMENTARIAS

LÍMITE DEL TÉRMINO MUNICIPAL

••••• DELIMITACIÓN DE SUELO URBANO

DELIMITACIÓN DE SECTORES, ÁREAS DE REFORMA INTERIOR,
ÁREAS DE TRANSFERENCIA DE APROVECHAMIENTO, ACTUACIONES SIMPLES Y
ÁREAS DE PLANEAMIENTO INCORPORADO

	SOU	SECTOR DE SUELO URBANO
	ARI	ÁREA DE REFORMA INTERIOR
	ATA	ÁREA DE TRANSFERENCIA DE APROVECHAMIENTO
	AS	ACTUACIÓN SIMPLE DE VARIOS EQUIPAMIENTO O ESPACIOS LIBRES
	API	ÁREA DE PLANEAMIENTO INCORPORADO

DELIMITACIÓN DE SUELO URBANIZABLE

	SUO	SUELO URBANIZABLE ORDENADO
	SUS	SUELO URBANIZABLE SECTORIZADO
	SUNS	SUELO URBANIZABLE NO SECTORIZADO

 DOMINIO PÚBLICO MARÍTIMO TERRESTRE  LÍMITE ZONA DE SERVIDUMBRE DE PROTECCIÓN  LÍMITE ZONA DE SERVIDUMBRE DE PROTECCIÓN EN CONJUNTO HISTÓRICO	
 DOMINIO PÚBLICO MARÍTIMO TERRESTRE PROBABLE  LÍMITE ZONA DE SERVIDUMBRE DE PROTECCIÓN PROBABLE  LÍMITE ZONA DE SERVIDUMBRE DE PROTECCIÓN EN CONJUNTO HISTÓRICO	
 ALINEACIÓN EXTERIOR  ALINEACIÓN INTERIOR Y/O RETRANQUEOS OBLIGATORIOS  FONDO MÁXIMO EDIFICABLE Y PASAJE EN PLANTA BAJA  CAMBIO DE ALTURA Y/O ZONA DE ORDENANZA	11-11
 ALTURA MÁXIMA  CONSERVACIÓN DE USO EXISTENTE	11-12
 SISTEMA GENERAL  MURALLA. RESTOS EMERGENTES	11-13

11-11	12-11	13-11
11-12	12-12	13-12
11-13	12-13	13-13

ORDENACIÓN

ORDENACIÓN PROMENORIZADA COMPLETA

escala 1/2.000

OPS
OFICINA DEL PLAN DE SEVILLA

gerencia de urbanismo EXCMO. AYUNTAMIENTO / NUEVO PLAN GENERAL DE ORDENACIÓN URBANÍSTICA. SEVILLA