


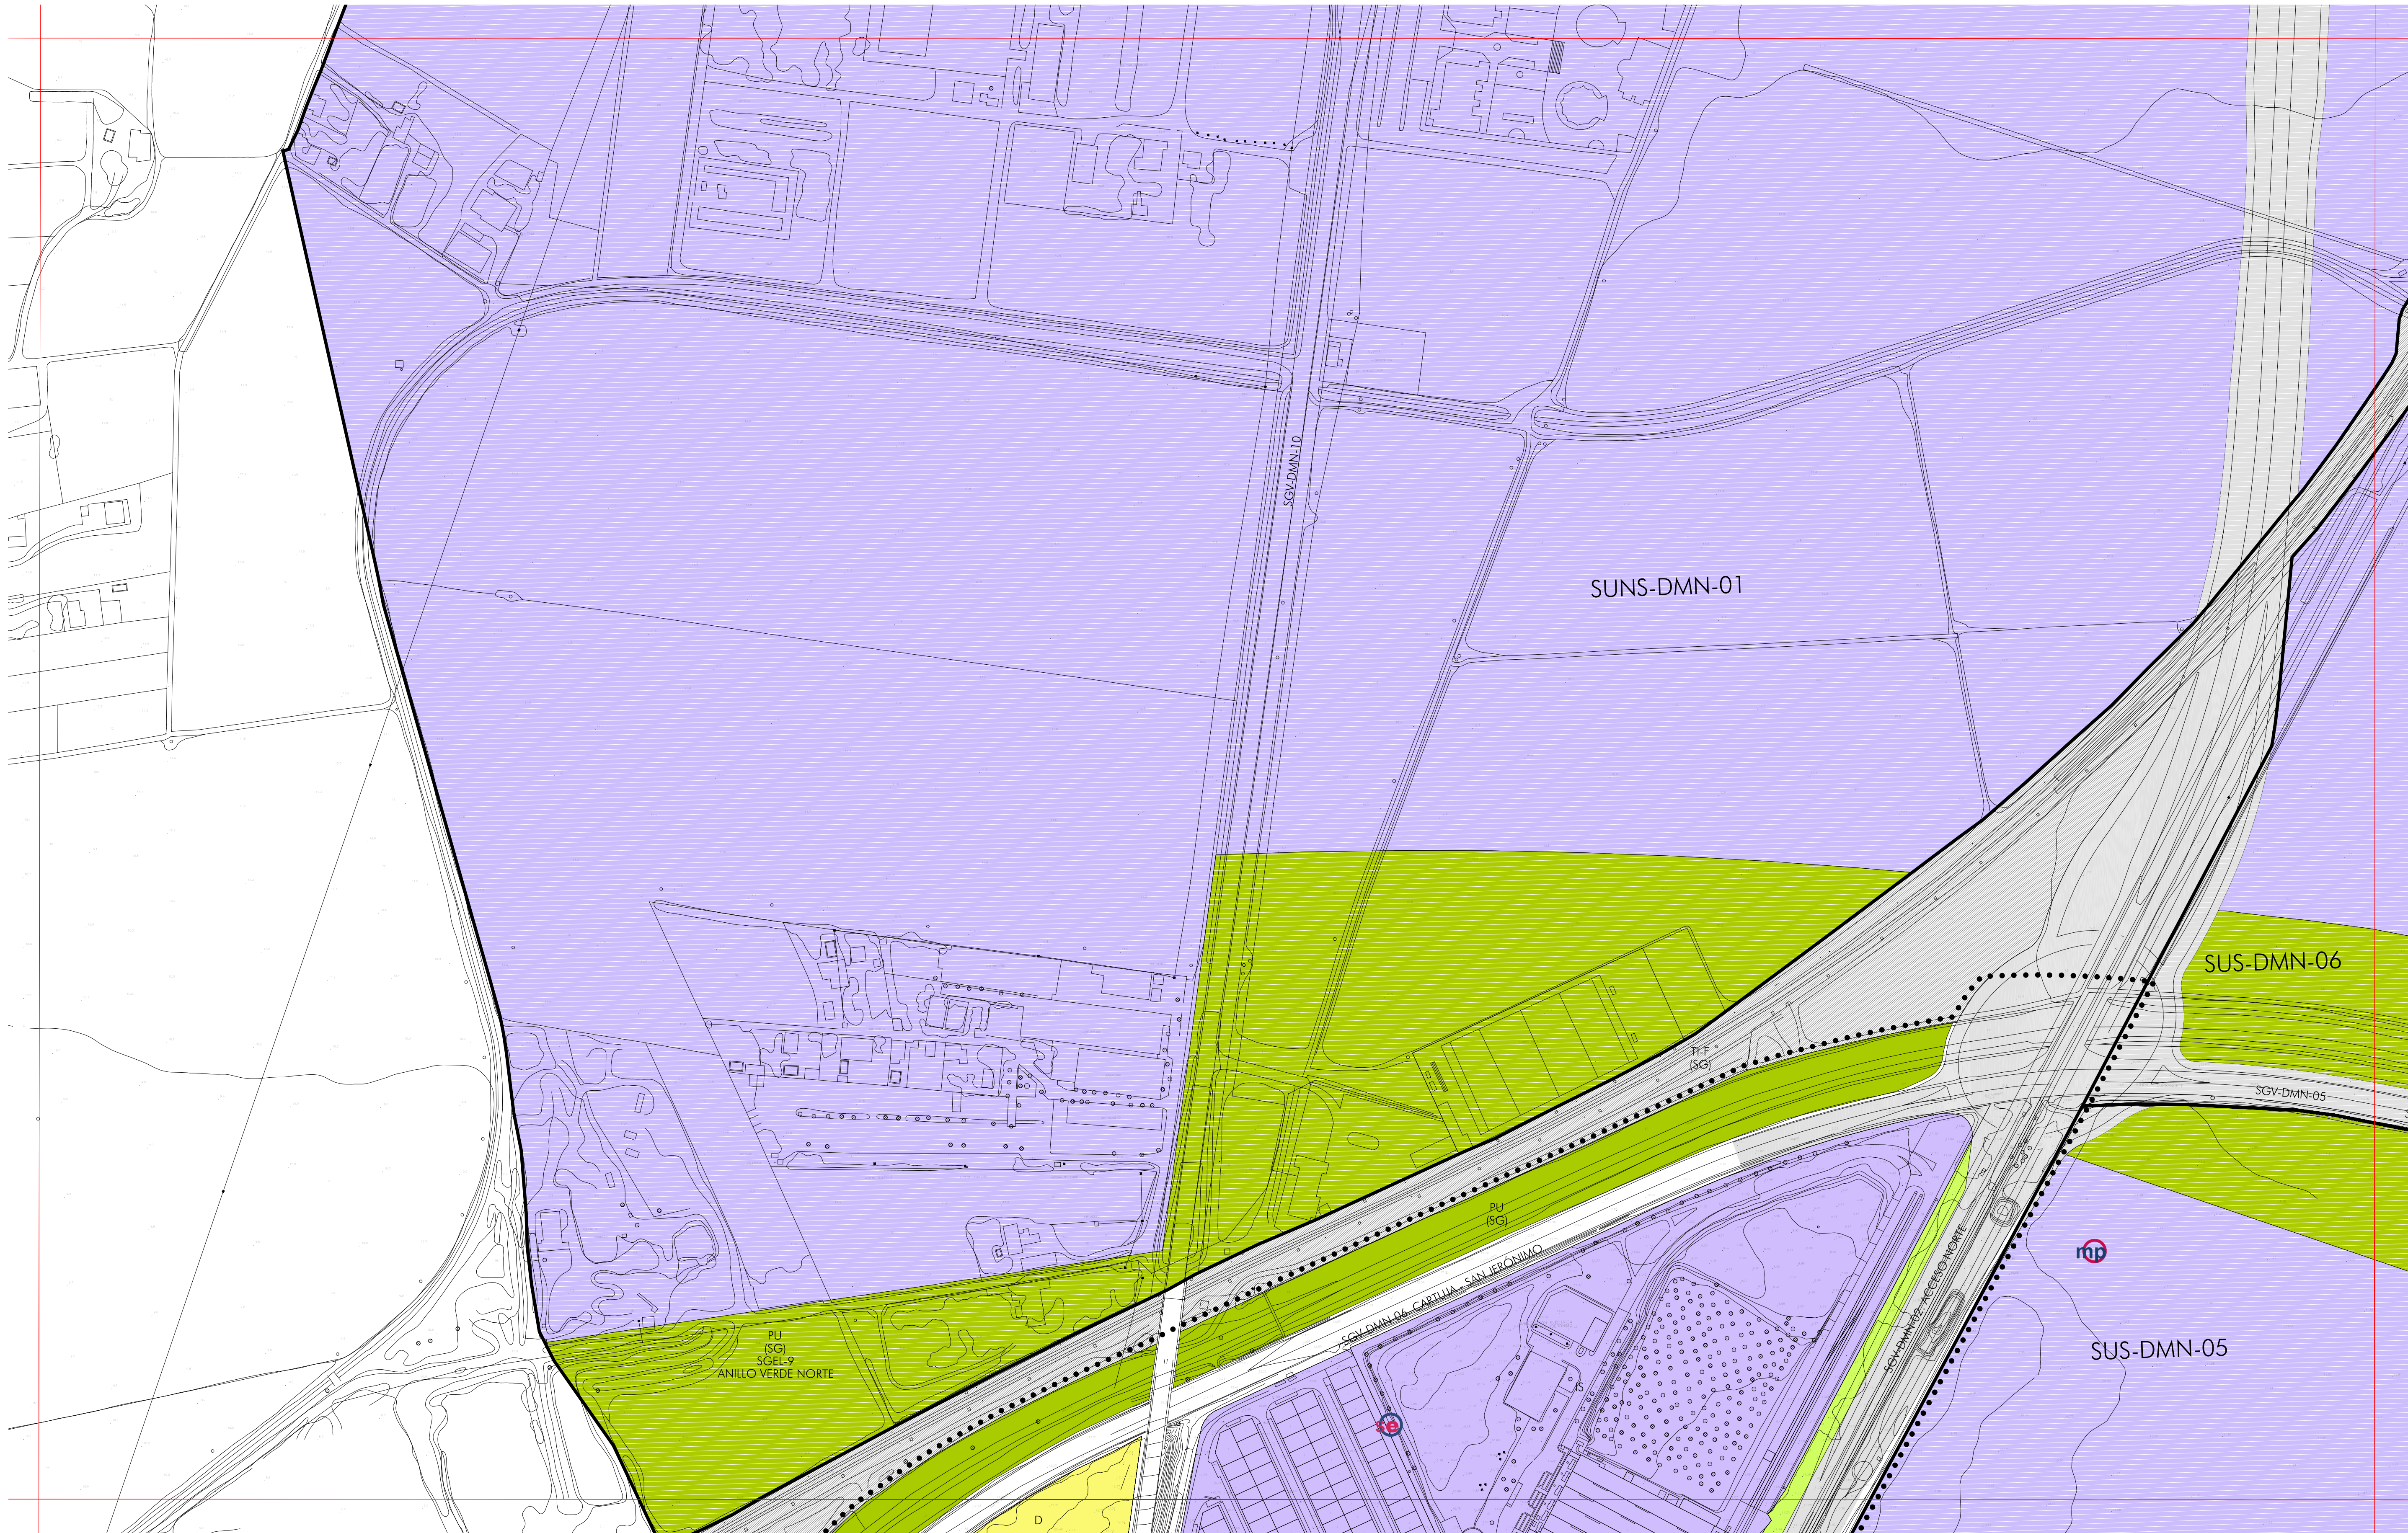

USOS GLOBALES Y PORMENORIZADOS

RESIDENCIAL
VIVIENDA

TERCIARIO
SERVICIOS TERCARIOS

ACTIVIDADES PRODUCTIVAS
SERVICIOS AVANZADOS

GRAN SUPERFICIE COMERCIAL

ESTACIÓN DE SERVICIO

INDUSTRIA Y ALMACENAMIENTO

DOTACIONAL
EQUIPAMIENTOS Y SERVICIOS PÚBLICOS

ESPACIOS LIBRES
PU PARQUE METROPOLITANO
PUJ PARQUE URBANO
ZV ZONAS VERDES

TRANSPORTES E INFRAESTRUCTURAS BÁSICAS
TI-SI SERVICIOS
TI-AP INFRAESTRUCTURAS
TI-CTM CENTRO DE TRANSPORTE DE MERCANCÍAS

VIARIO PROPUESTO

ESPACIO LIBRE ASOCIADO AL VIARIO

T-F FERROVIARIO
T-P PUERTO
T-AP AEROPUERTO
T-HIP HUELPUERTO
T-IT INTERCAMBIADOR DE TRANSPORTE

S-S
S-BS
S-EA
S-SC
S-SP
S-EES

ZONAS DE ORDENANZAS DEL SUELO URBANO

CH CENTRO HISTÓRICO
M EDIFICACIÓN EN MANZANA
MP EDIFICACIÓN EN MANZANA CON ALINEACIÓN INTERIOR OBLIGATORIA O MÁXIMA
A EDIFICACIÓN ABIERTA
SB SUBURBANA
CJ CIUDAD JARDÍN
AD UNIFAMILIAR ADOSADA
UA UNIFAMILIAR AISLADA Y/O AGRUPIADA
CT CONSERVACIÓN TIPOLOGICA
IS INDUSTRIA SINGULAR
IA INDUSTRIA EN EDIFICACIÓN ABIERTA
IC INDUSTRIA EN EDIFICACIÓN COMPACTA
SA SERVICIOS AVANZADOS
ST-A SERVICIOS TERCARIOS EN EDIFICACIÓN ABIERTA
ST-C SERVICIOS TERCARIOS EN EDIFICACIÓN COMPACTA

CLASIFICACIÓN Y CATEGORÍAS DE SUELO. DETERMINACIONES COMPLEMENTARIAS

LÍMITE DEL TÉRMINO MUNICIPAL

DELIMITACIÓN DE SUELO URBANO

DELIMITACIÓN DE SUELO URBANIZABLE

DOMINIO PÚBLICO MARÍTIMO TERRESTRE
LÍMITE ZONA DE SERVIDUMBRE DE PROTECCIÓN
LÍMITE ZONA DE SERVIDUMBRE DE PROTECCIÓN EN CONJUNTO HISTÓRICO

DOMINIO PÚBLICO MARÍTIMO TERRESTRE PROBABLE
LÍMITE ZONA DE SERVIDUMBRE DE PROTECCIÓN PROBABLE
LÍMITE ZONA DE SERVIDUMBRE DE PROTECCIÓN PROBABLE EN CONJUNTO HISTÓRICO

ALINEACIÓN EXTERIOR
ALINEACIÓN INTERIOR Y/O RETRANQUEOS OBLIGATORIOS
FONDO MÁXIMO EDIFICABLE Y PASAJE EN PLANTA BAJA
CAMBIO DE ALTURA Y/O ZONA DE ORDENANZA

ALTURA MÁXIMA
CONSERVACIÓN DE USO EXISTENTE
SISTEMA GENERAL
MURALLA. RESTOS EMERGENTES

	13-07	14-07
	13-08	14-08
12-09	13-09	14-09

ORDENACIÓN

ORDENACIÓN PORMENORIZADA COMPLETA

escala 1/2.000

OPS
OPERAÇÕES DE PLANEAMENTO E GESTÃO DE TERRITÓRIO

gerencia de urbanismo EXCMO. AYUNTAMIENTO / NUEVO PLAN GENERAL DE ORDENACIÓN URBANÍSTICA. SEVILLA