


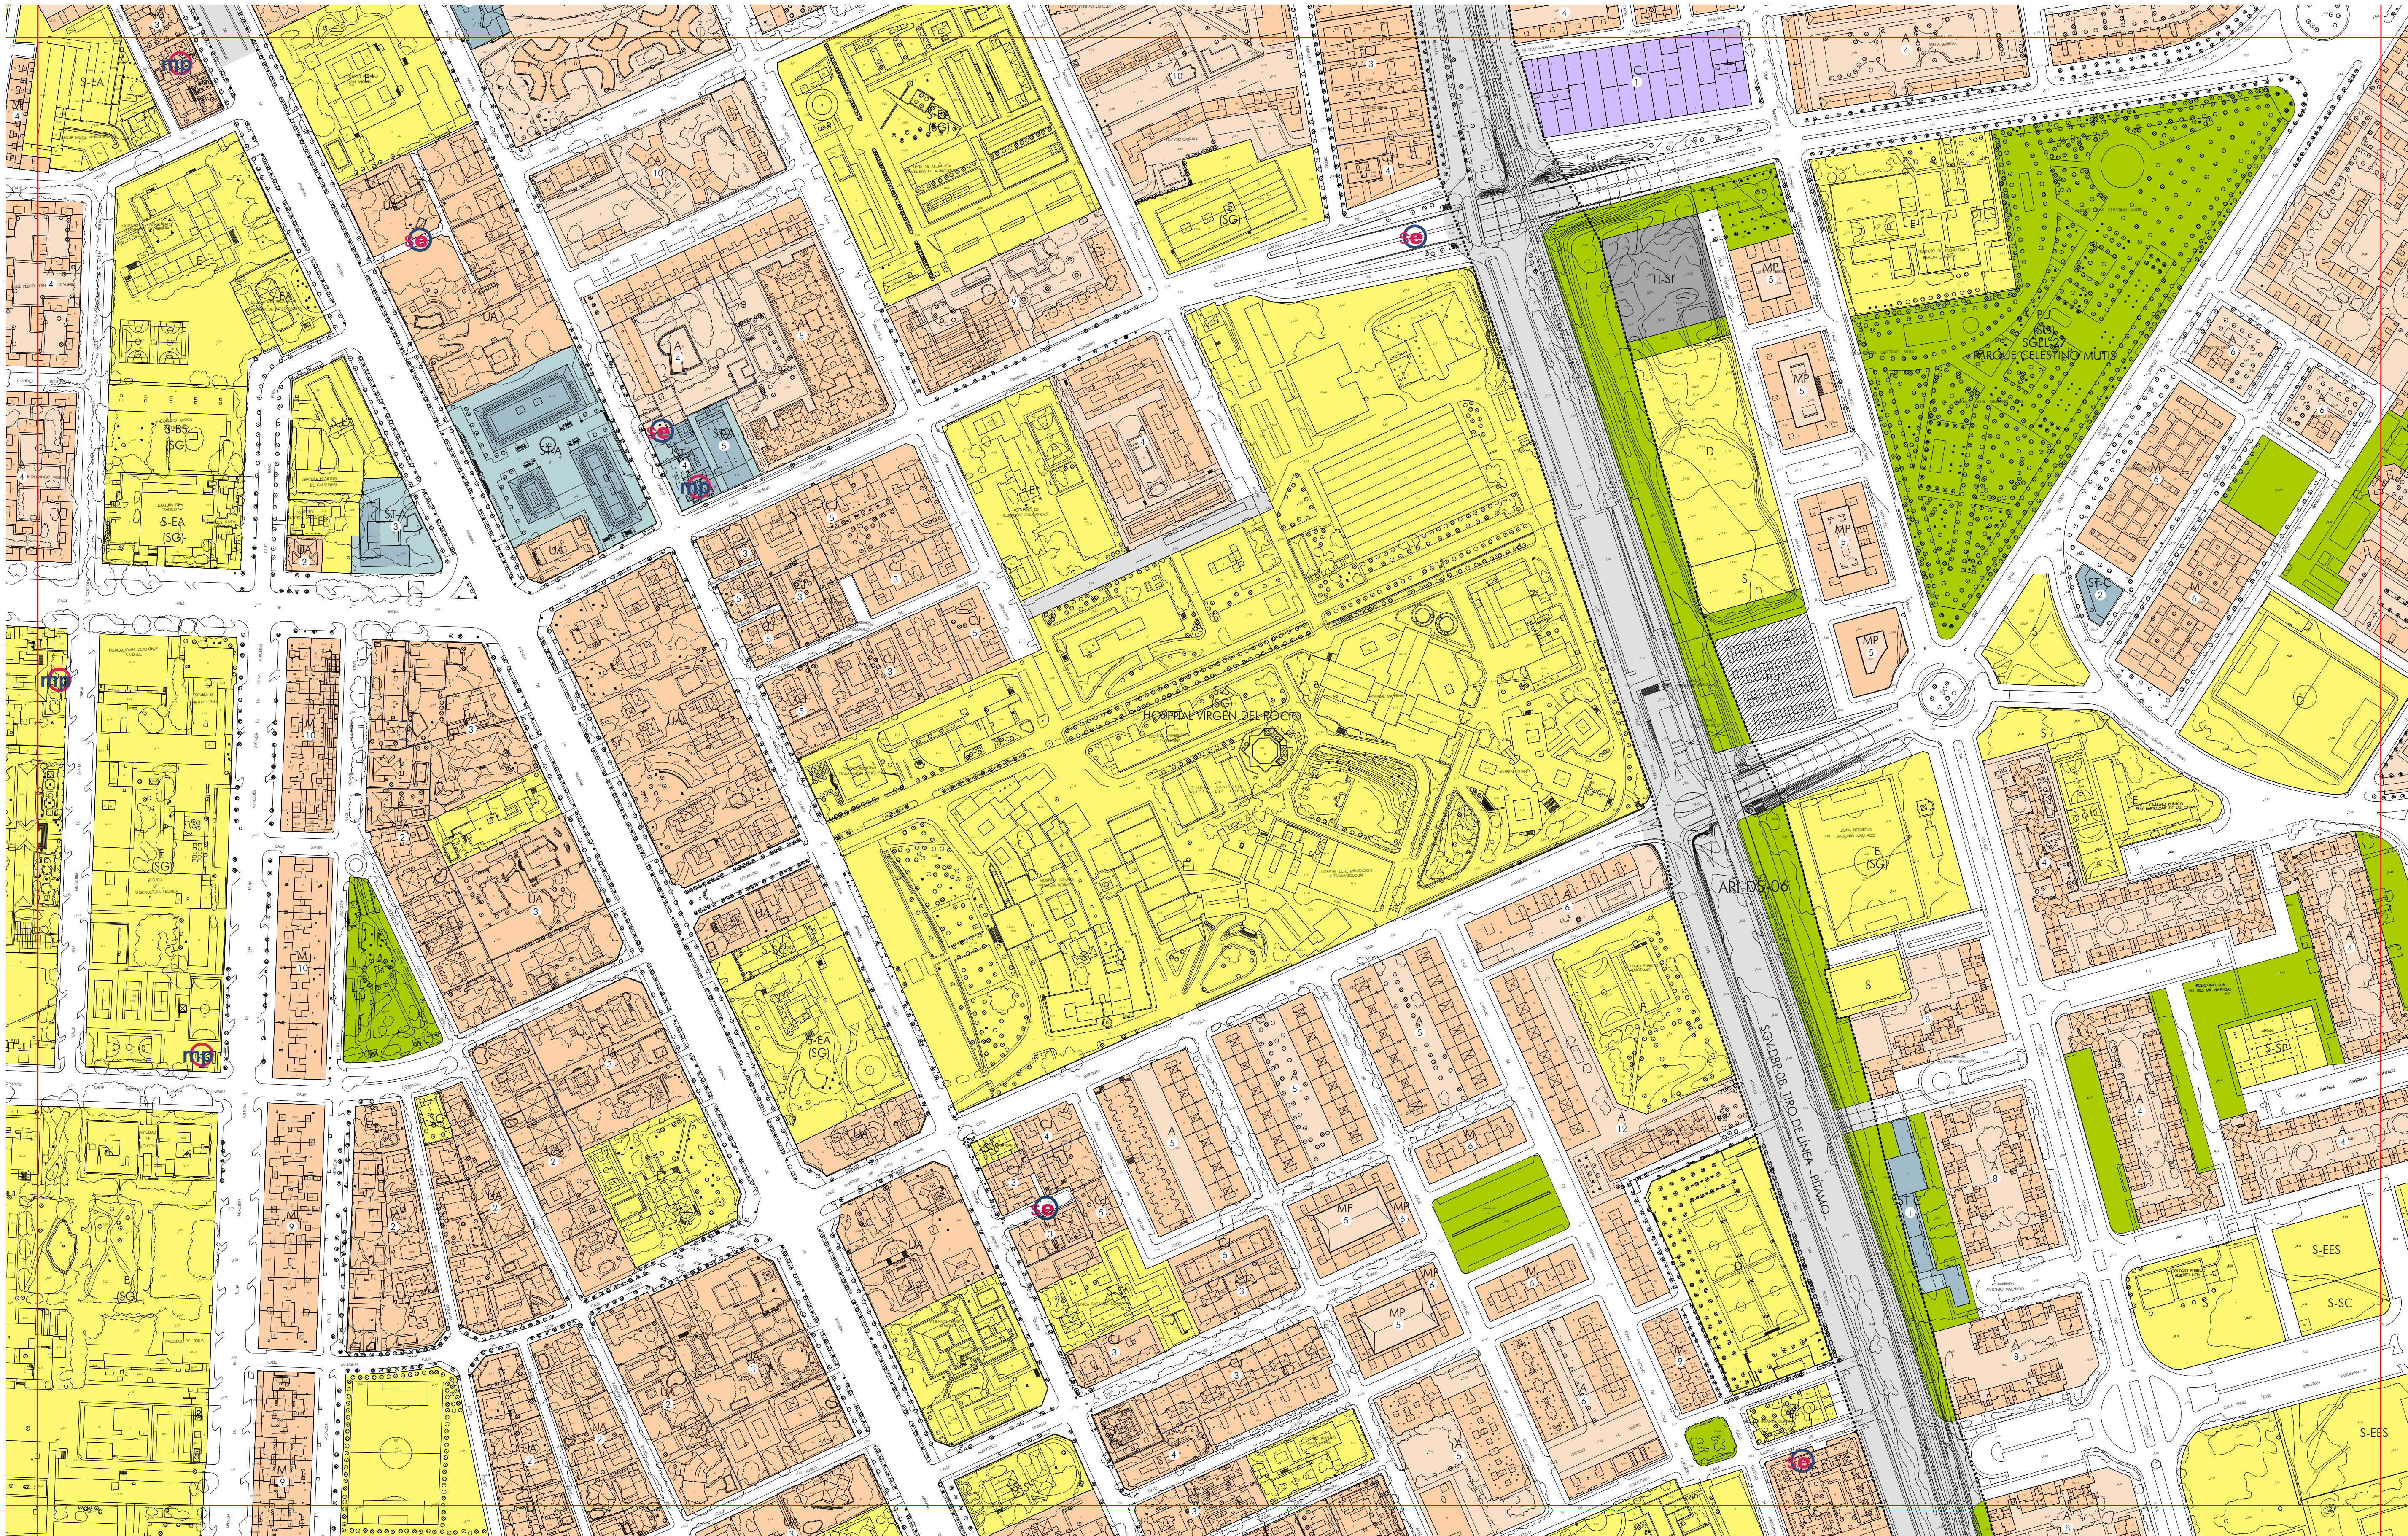

USOS GLOBALES Y PORMENORIZADOS

RESIDENCIAL

- VIVIENDA
- TERCIARIO
- SERVICIOS TERCARIOS
- GRAN SUPERFICIE COMERCIAL
- ESTACIÓN DE SERVICIO

ACTIVIDADES PRODUCTIVAS

- SERVICIOS AVANZADOS
- INDUSTRIA Y ALMACENAMIENTO

DOTACIONAL

- EQUIPAMIENTOS Y SERVICIOS PÚBLICOS
- EDUCATIVO
- DEPORTIVO
- SERVICIOS DE INTERÉS PÚBLICO Y SOCIAL
- SERVICIOS DE CARÁCTER PRIVADO
- ESPACIOS LIBRES
- PARQUE METROPOLITANO
- PARQUE URBANO
- ZONAS VERDES
- TRANSPORTES E INFRAESTRUCTURAS BÁSICAS
- TI-SI
- SERVICIOS INFRAESTRUCTURALES
- TI-CTM
- CENTRO DE TRANSPORTE DE MERCANCÍAS
- VIARIO PROPUESTO
- ESPACIO LIBRE ASOCIADO AL VIARIO

ZONAS DE ORDENANZAS DEL SUELO URBANO

- CH CENTRO HISTÓRICO
- M EDIFICACIÓN EN MANZANA
- MP EDIFICACIÓN EN MANZANA
- CON ALINEACIÓN INTERIOR OBLIGATORIA O MÁXIMA
- EDIFICACIÓN ABIERTA
- AB SUBURBANA
- CJ CIUDAD JARDÍN
- AD UNIFAMILIAR ADOSADA
- UA UNIFAMILIAR AISLADA Y/O AGRUPADA
- CT CONSERVACIÓN TIPOLOGICA
- IS INDUSTRIA SINGULAR
- IA INDUSTRIA EN EDIFICACIÓN ABIERTA
- IC INDUSTRIA EN EDIFICACIÓN COMPACTA
- SA SERVICIOS AVANZADOS
- STA SERVICIOS TERCARIOS EN EDIFICACIÓN ABIERTA
- ST-C SERVICIOS TERCARIOS EN EDIFICACIÓN COMPACTA

CLASIFICACIÓN Y CATEGORÍAS DE SUELO. DETERMINACIONES COMPLEMENTARIAS

- LÍMITE DEL TÉRMINO MUNICIPAL
- DELIMITACIÓN DE SECTORES, ÁREAS DE REFORMA INTERIOR, ÁREAS DE TRANSFERENCIA DE APROVECHAMIENTO, ACTUACIONES SIMPLES Y ÁREAS DE PLANEAMIENTO INCORPORADO
- SOU SECTOR DE SUELO URBANO
- ARI ÁREA DE REFORMA INTERIOR
- ATA ÁREA DE TRANSFERENCIA DE APROVECHAMIENTO
- AS ACTUACIÓN SIMPLE DE VARIO, EQUIPAMIENTO O ESPACIOS LIBRES
- ARI ÁREA DE PLANEAMIENTO INCORPORADO
- DELIMITACIÓN DE SUELO URBANIZABLE
- SUO SUELO URBANIZABLE ORDENADO
- SUS SUELO URBANIZABLE SECTORIZADO
- SUNS SUELO URBANIZABLE NO SECTORIZADO
- DOMINIO PÚBLICO MARITIMO TERRESTRE
- LÍMITE ZONA DE SERVIDUMBRE DE PROTECCIÓN
- LÍMITE ZONA DE SERVIDUMBRE DE PROTECCIÓN EN CONJUNTO HISTÓRICO
- DOMINIO PÚBLICO MARITIMO TERRESTRE PROBABLE
- LÍMITE ZONA DE SERVIDUMBRE DE PROTECCIÓN PROBABLE
- LÍMITE ZONA DE SERVIDUMBRE DE PROTECCIÓN PROBABLE EN CONJUNTO HISTÓRICO
- ALINEACIÓN EXTERIOR
- ALINEACIÓN INTERIOR Y/O RETRANQUEOS OBLIGATORIOS
- FONDO MÁXIMO EDIFICABLE Y PASAJE EN PLANTA BAJA
- CAMBIO DE ALTURA Y/O ZONA DE ORDENANZA
- ALTURA MÁXIMA
- CONSERVACIÓN DE USO EXISTENTE
- SISTEMA GENERAL
- MURALLA. RESTOS EMERGENTES

12-16	13-16	14-16
12-17	13-17	14-17
12-18	13-18	14-18

ORDENACIÓN PORMENORIZADA COMPLETA

escala 1/2.000

OPS

OFICINA DEL PLAN DE SEVILLA
gerencia de urbanismo EXCMO. AYUNTAMIENTO / NUEVO PLAN GENERAL DE ORDENACIÓN URBANÍSTICA SEVILLA

ORDENACIÓN