TEXTO REFUNDIDO
Documento aprobado definitivamente por Acuerdo Plenario del Ayuntamiento de Sevilla de 15 de marzo de 2007

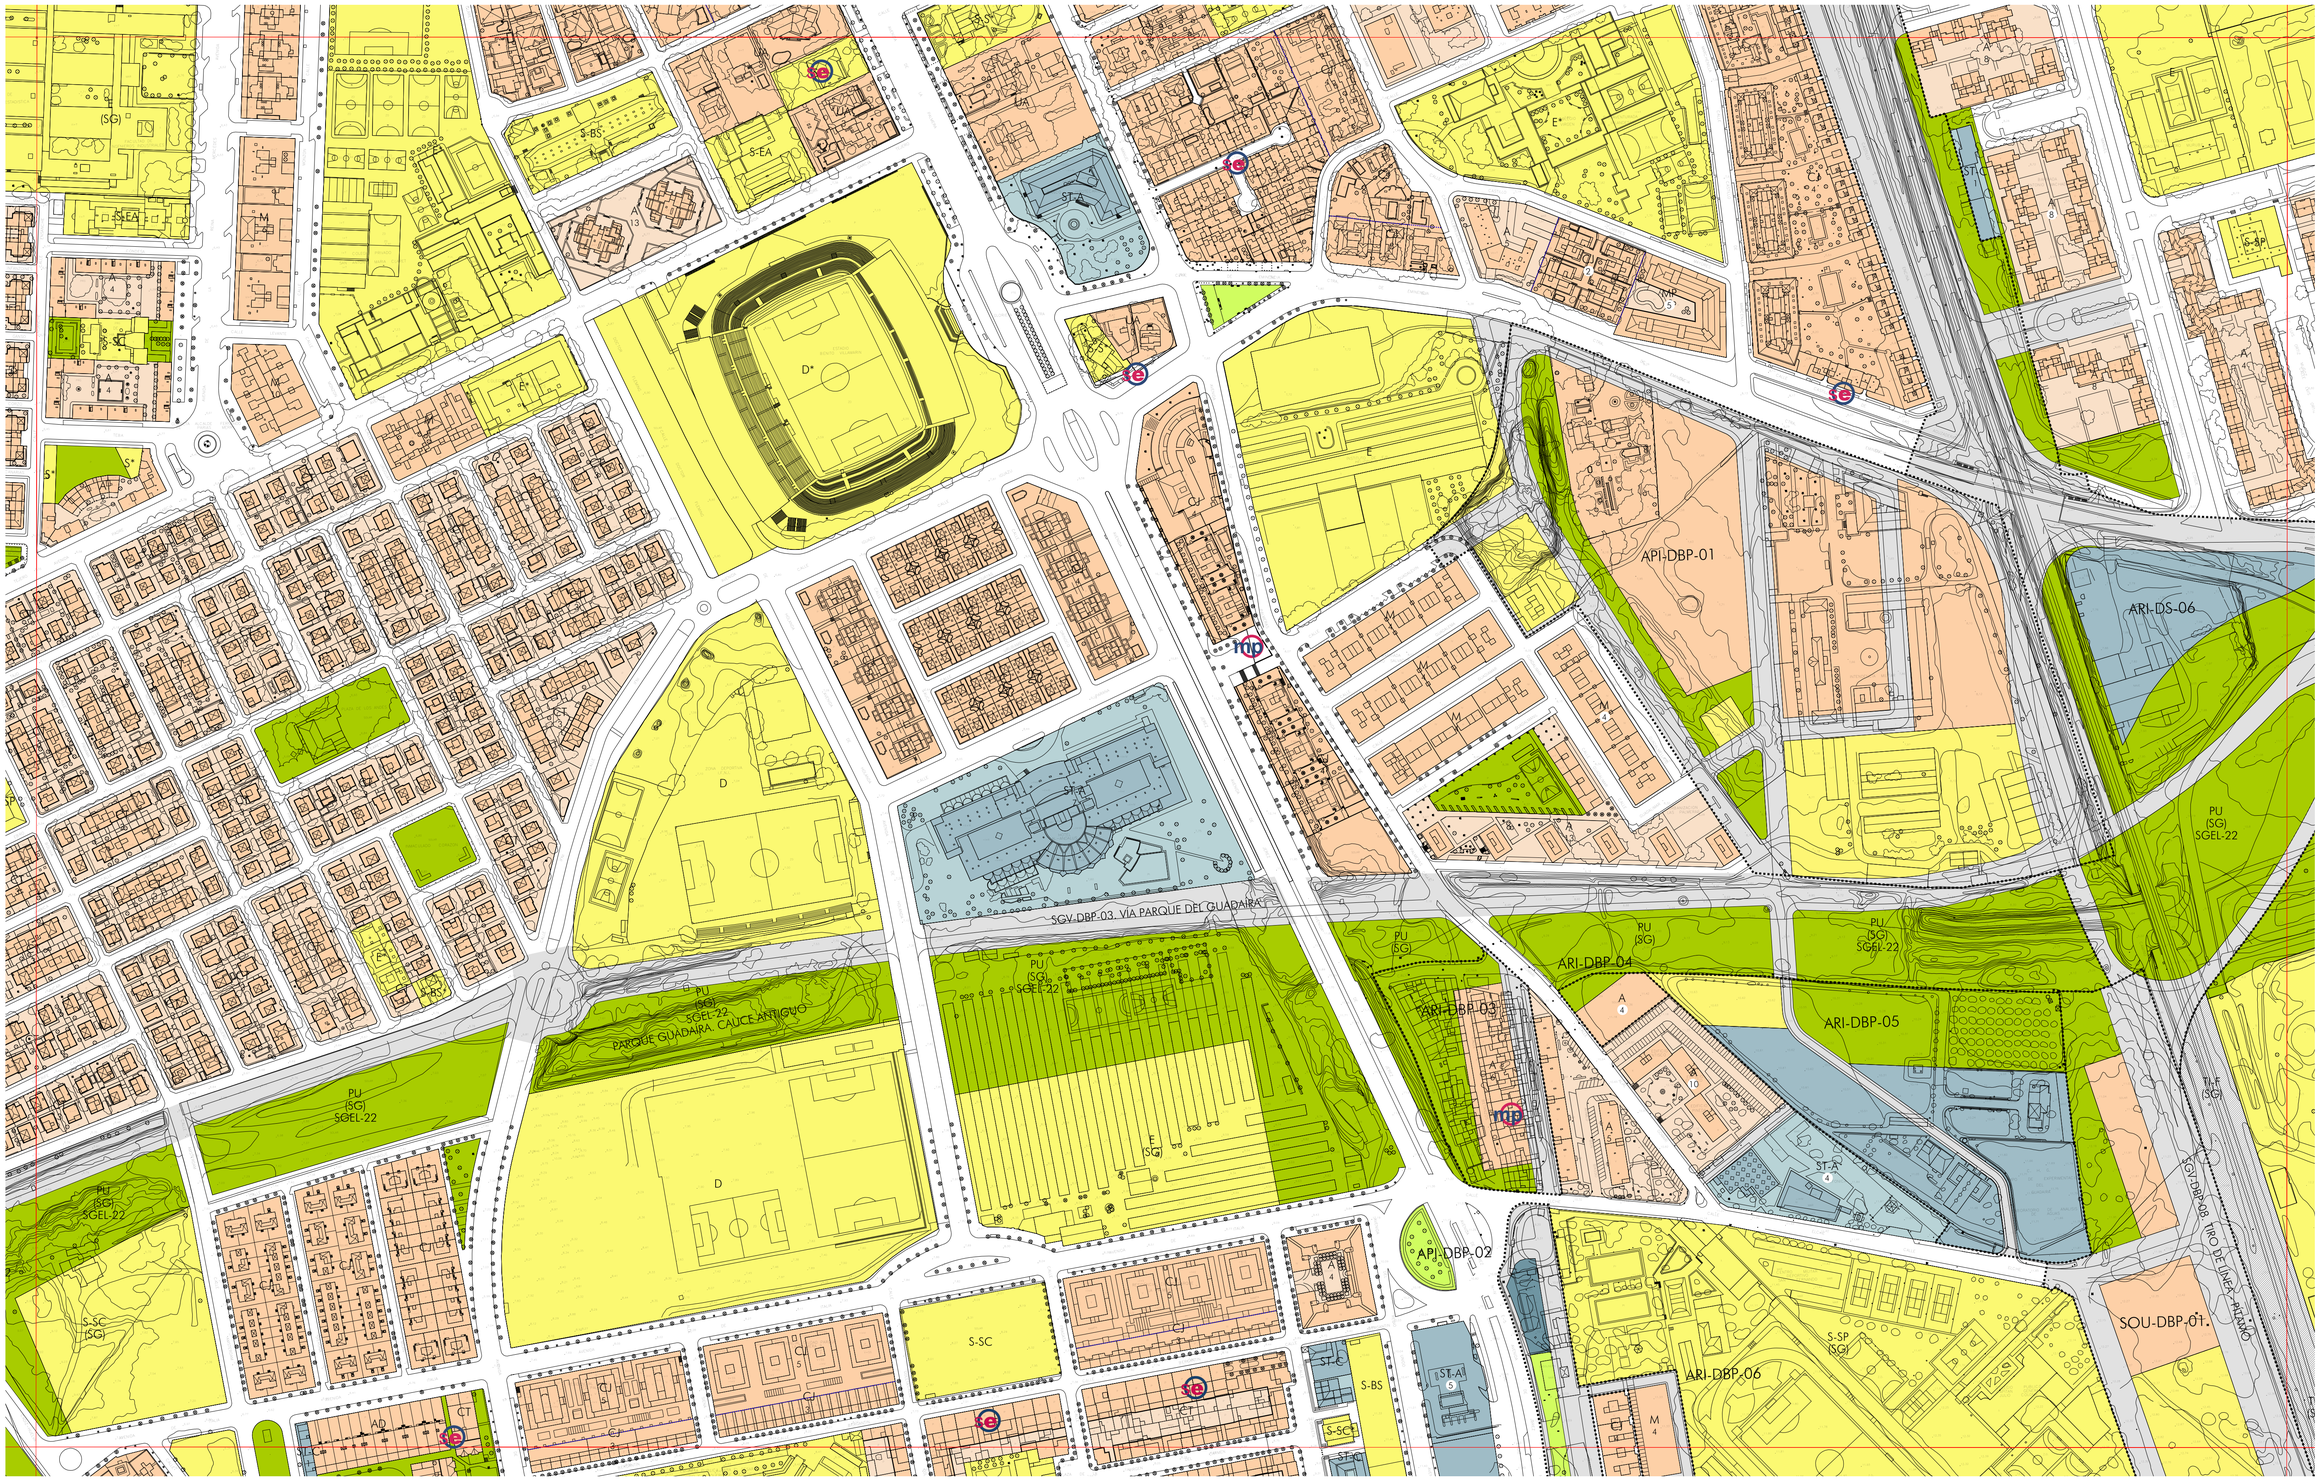

USOS GLOBALES Y PORMENORIZADOS

RESIDENCIAL
VIVIENDA

TERCIARIO
SERVICIOS TERCIARIOS
GRAN SUPERFICIE COMERCIAL
ESTACIÓN DE SERVICIO

ACTIVIDADES PRODUCTIVAS
SERVICIOS AVANZADOS
INDUSTRIA Y ALMACENAMIENTO

DOTACIONAL
EQUIPAMIENTOS Y SERVICIOS PÚBLICOS
- E EDUCATIVO
- D DEPORTIVO
- S SERVICIOS DE INTERÉS PÚBLICO Y SOCIAL
- (*) DE CARÁCTER PRIVADO

S-S, S-BS, S-EA, S-SC, S-SP, S-EES

ESPACIOS LIBRES
- PM PARQUE METROPOLITANO
- PU PARQUE URBANO
- ZV ZONAS VERDES

TRANSPORTES E INFRAESTRUCTURAS BÁSICAS
- TI-SI SERVICIOS INFRAESTRUCTURALES
- TI-CTM CENTRO DE TRANSPORTE DE MERCANCÍAS
- TI-F FERROVIARIO
- TI-P PUERTO
- TI-AP AEROPUERTO
- TI-HP HELIPUERTO
- TI-IT INTERCAMBIADOR DE TRANSPORTE

VIARIO PROPUESTO
ESPACIO LIBRE ASOCIADO AL VIARIO

ZONAS DE ORDENANZAS DEL SUELO URBANO

- **CH** CENTRO HISTÓRICO
- **M** EDIFICACIÓN EN MANZANA
- **MP** EDIFICACIÓN EN MANZANA CON ALINEACIÓN INTERIOR OBLIGATORIA O MÁXIMA
- **A** EDIFICACIÓN ABIERTA
- **SB** SUBURBANA
- **CJ** CIUDAD JARDÍN
- **AD** UNIFAMILIAR ADOSADA
- **UA** UNIFAMILIAR AISLADA Y/O AGRUPADA
- **CT** CONSERVACIÓN TIPOLÓGICA
- **IS** INDUSTRIA SINGULAR
- **IA** INDUSTRIA EN EDIFICACIÓN ABIERTA
- **IC** INDUSTRIA EN EDIFICACIÓN COMPACTA
- **SA** SERVICIOS AVANZADOS
- **ST-A** SERVICIOS TERCIARIOS EN EDIFICACIÓN ABIERTA
- **ST-C** SERVICIOS TERCIARIOS EN EDIFICACIÓN COMPACTA

CLASIFICACIÓN Y CATEGORÍAS DE SUELO. DETERMINACIONES COMPLEMENTARIAS

LÍMITE DEL TÉRMINO MUNICIPAL
DELIMITACIÓN DE SUELO URBANO

DELIMITACIÓN DE SECTORES, ÁREAS DE REFORMA INTERIOR, ÁREAS DE TRANSFERENCIA DE APROVECHAMIENTO, ACTUACIONES SIMPLES Y ÁREAS DE PLANEAMIENTO INCORPORADO

- SOU SECTOR DE SUELO URBANO
- ARI ÁREA DE REFORMA INTERIOR
- ATA ÁREA DE TRANSFERENCIA DE APROVECHAMIENTO
- AS ACTUACIÓN SIMPLE DE VIARIO, EQUIPAMIENTO O ESPACIOS LIBRES
- API ÁREA DE PLANEAMIENTO INCORPORADO

DELIMITACIÓN DE SUELO URBANIZABLE

- SUO SUELO URBANIZABLE ORDENADO
- SUS SUELO URBANIZABLE SECTORIZADO
- SUNS SUELO URBANIZABLE NO SECTORIZADO

DOMINIO PÚBLICO MARÍTIMO TERRESTRE
LÍMITE ZONA DE SERVIDUMBRE DE PROTECCIÓN
LÍMITE ZONA DE SERVIDUMBRE DE PROTECCIÓN EN CONJUNTO HISTÓRICO

DOMINIO PÚBLICO MARÍTIMO TERRESTRE PROBABLE
LÍMITE ZONA DE SERVIDUMBRE DE PROTECCIÓN PROBABLE
LÍMITE ZONA DE SERVIDUMBRE DE PROTECCIÓN PROBABLE EN CONJUNTO HISTÓRICO

ALINEACIÓN EXTERIOR
ALINEACIÓN INTERIOR Y/O RETRANQUEOS OBLIGATORIOS
FONDO MÁXIMO EDIFICABLE Y PASAJE EN PLANTA BAJA
CAMBIO DE ALTURA Y/O ZONA DE ORDENANZA

(2) ALTURA MÁXIMA
▲ CONSERVACIÓN DE USO EXISTENTE
(SG) SISTEMA GENERAL
MURALLA. RESTOS EMERGENTES

12-17	13-17	14-17
12-18	13-18	14-18
12-19	13-19	14-19

ORDENACIÓN

ORDENACIÓN PORMENORIZADA COMPLETA

escala 1/2.000

OPS OFICINA DEL PLAN DE SEVILLA

gerencia de urbanismo EXCMO. AYUNTAMIENTO / NUEVO PLAN GENERAL DE ORDENACIÓN URBANÍSTICA. SEVILLA