


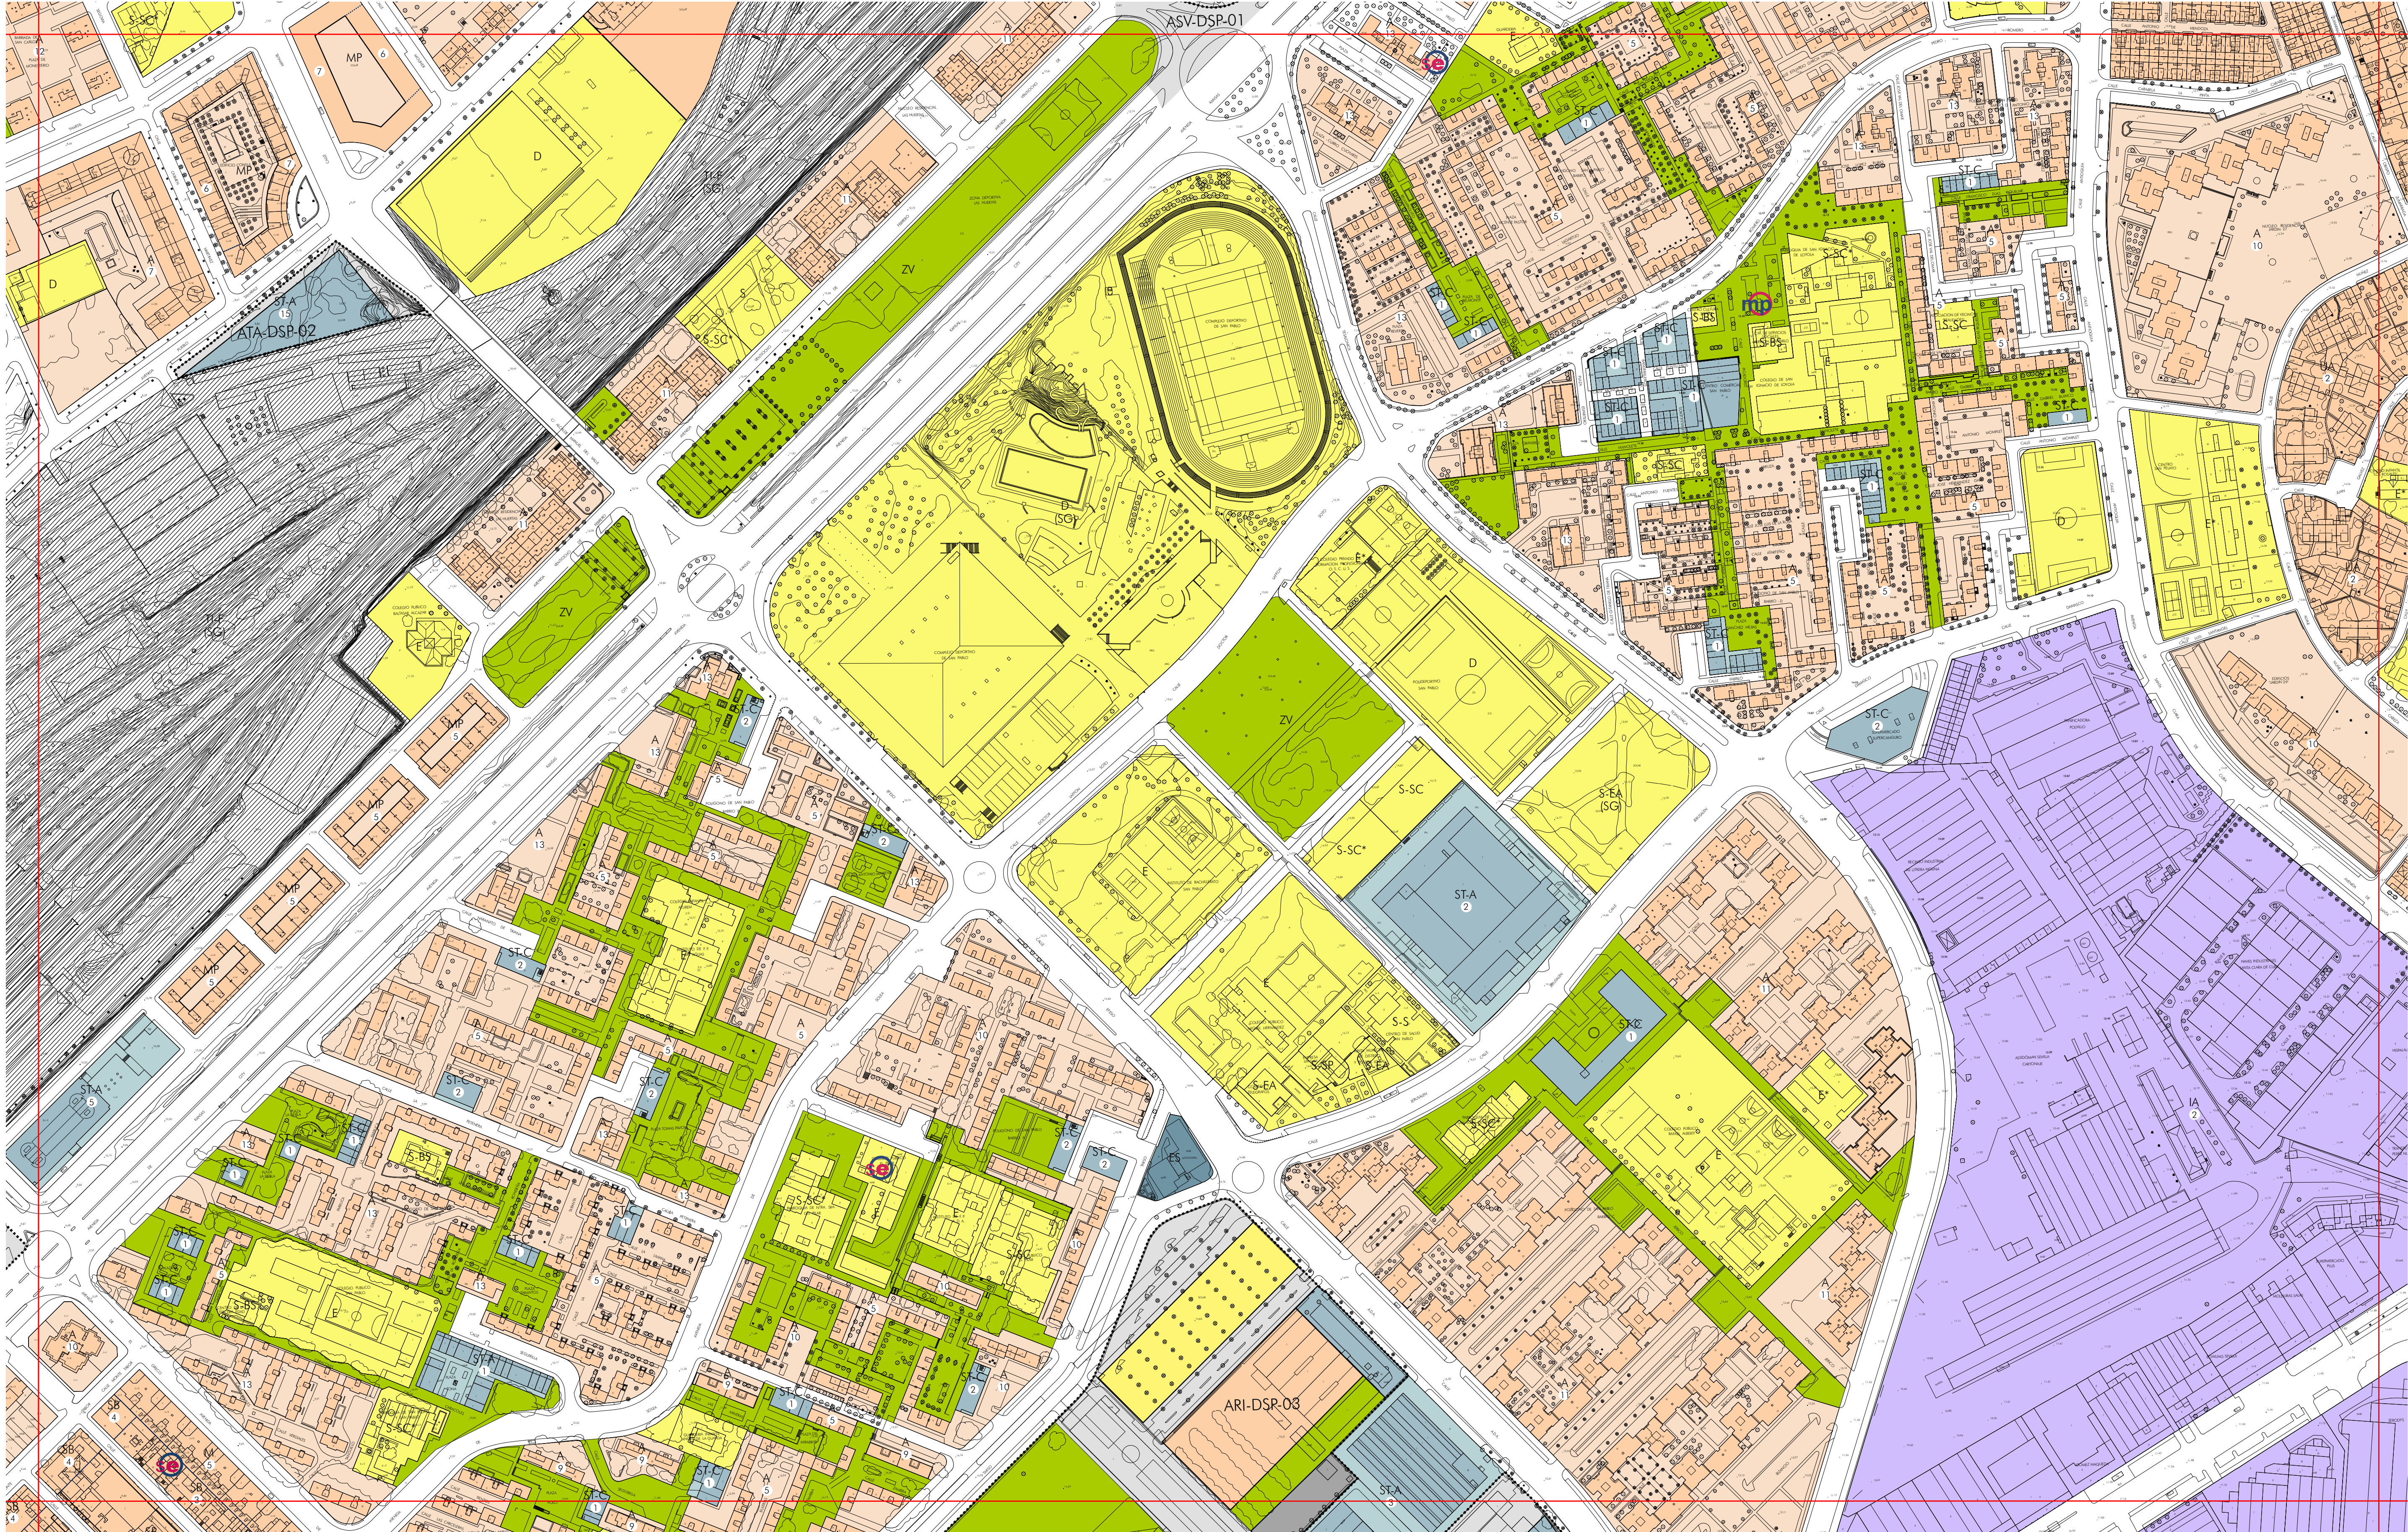

USOS GLOBALES Y PORMENORIZADOS

RESIDENCIAL

VIVIENDA

GRAN SUPERFICIE

ESTACIÓN DE SERVICIO

SERVICIOS TERCARIOS

INDUSTRIA Y ALMACENAMIENTO

ACTIVIDADES PRODUCTIVAS

SERVICIOS AVANZADOS

INDUSTRIA Y ALMACENAMIENTO

INDUSTRIA Y ALMACENAMIENTO

INDUSTRIA Y ALMACENAMIENTO

DOTACIONAL

EQUIPAMIENTOS Y SERVICIOS PÚBLICOS

E EDUCATIVO

D DEPORTIVO

S SERVICIOS DE INTERÉS PÚBLICO Y SOCIAL

(*) DE CARÁCTER PRIVADO

ESPACIOS LIBRES

PM PARQUE METROPOLITANO

PJ PARQUE URBANO

ZV ZONAS VERDES

TRANSPORTES E INFRAESTRUCTURAS BÁSICAS

TI-SI SERVICIOS

TI-AP INFRAESTRUCTURAS

TI-CTM CENTRO DE TRANSPORTE DE MERCANCÍAS

VIARIO PROPUESTO

ESPACIO LIBRE ASOCIADO AL VIARIO

CH

CENTRO HISTÓRICO

M EDIFICACIÓN EN MANZANA

MP EDIFICACIÓN EN MANZANA

CON ALINEACIÓN INTERIOR OBLIGATORIA O MÁXIMA

A EDIFICACIÓN ABIERTA

SB SUBURBANA

CJ CIUDAD JARDÍN

AD UNIFAMILIAR ADOSADA

UA UNIFAMILIAR AISLADA Y/O AGRUPADA

CT CONSERVACIÓN TIPOLOGICA

IA INDUSTRIA SINGULAR

IS INDUSTRIA EN EDIFICACIÓN ABIERTA

IC INDUSTRIA EN EDIFICACIÓN COMPACTA

SA SERVICIOS AVANZADOS

ST-A SERVICIOS TERCARIOS EN EDIFICACIÓN ABIERTA

ST-C SERVICIOS TERCARIOS EN EDIFICACIÓN COMPACTA

ZONAS DE ORDENANZAS DEL SUELO URBANO

CLASIFICACIÓN Y CATEGORÍAS DE SUELO. DETERMINACIONES COMPLEMENTARIAS

— LÍMITE DEL TÉRMINO MUNICIPAL

..... DELIMITACIÓN DE SUELO URBANO

DELIMITACIÓN DE SECTORES, ÁREAS DE REFORMA INTERIOR, ÁREAS DE TRANSFERENCIA DE APROVECHAMIENTO, ACTUACIONES SIMPLES Y ÁREAS DE PLANEAMIENTO INCORPORADO

SOU SECTOR DE SUELO URBANO

ARI ÁREA DE REFORMA INTERIOR

ATA ÁREA DE TRANSFERENCIA DE APROVECHAMIENTO

AS ACTUACIÓN SIMPLE DE VARIO, EQUIPAMIENTO O ESPACIOS LIBRES

API ÁREA DE PLANEAMIENTO INCORPORADO

DELIMITACIÓN DE SUELO URBANIZABLE

SUO SUELO URBANIZABLE ORDENADO

SUS SUELO URBANIZABLE SECTORIZADO

SUNS SUELO URBANIZABLE NO SECTORIZADO

DOMINIO PÚBLICO MARÍTIMO TERRESTRE

LÍMITE ZONA DE SERVIDUMBRE DE PROTECCIÓN

LÍMITE ZONA DE SERVIDUMBRE DE PROTECCIÓN EN CONJUNTO HISTÓRICO

DOMINIO PÚBLICO MARÍTIMO TERRESTRE PROBABLE

LÍMITE ZONA DE SERVIDUMBRE DE PROTECCIÓN PROBABLE

LÍMITE ZONA DE SERVIDUMBRE DE PROTECCIÓN PROBABLE EN CONJUNTO HISTÓRICO

ALINEACIÓN EXTERIOR

ALINEACIÓN INTERIOR Y/O RETRANQUEOS OBLIGATORIOS

FONDO MÁXIMO EDIFICABLE Y PASAJE EN PLANTA BAJA

CAMBIO DE ALTURA Y/O ZONA DE ORDENANZA

2 ALTURA MÁXIMA

CONSERVACIÓN DE USO EXISTENTE

SISTEMA GENERAL

MURALLA. RESTOS EMERGENTES

13-12	14-12	15-12
13-13	14-13	15-13
13-14	14-14	15-14

ORDENACIÓN

ORDENACIÓN PORMENORIZADA COMPLETA

escala 1/2.000

OPS

gerencia de urbanismo EXCMO. AYUNTAMIENTO / NUEVO PLAN GENERAL DE ORDENACIÓN URBANÍSTICA. SEVILLA