


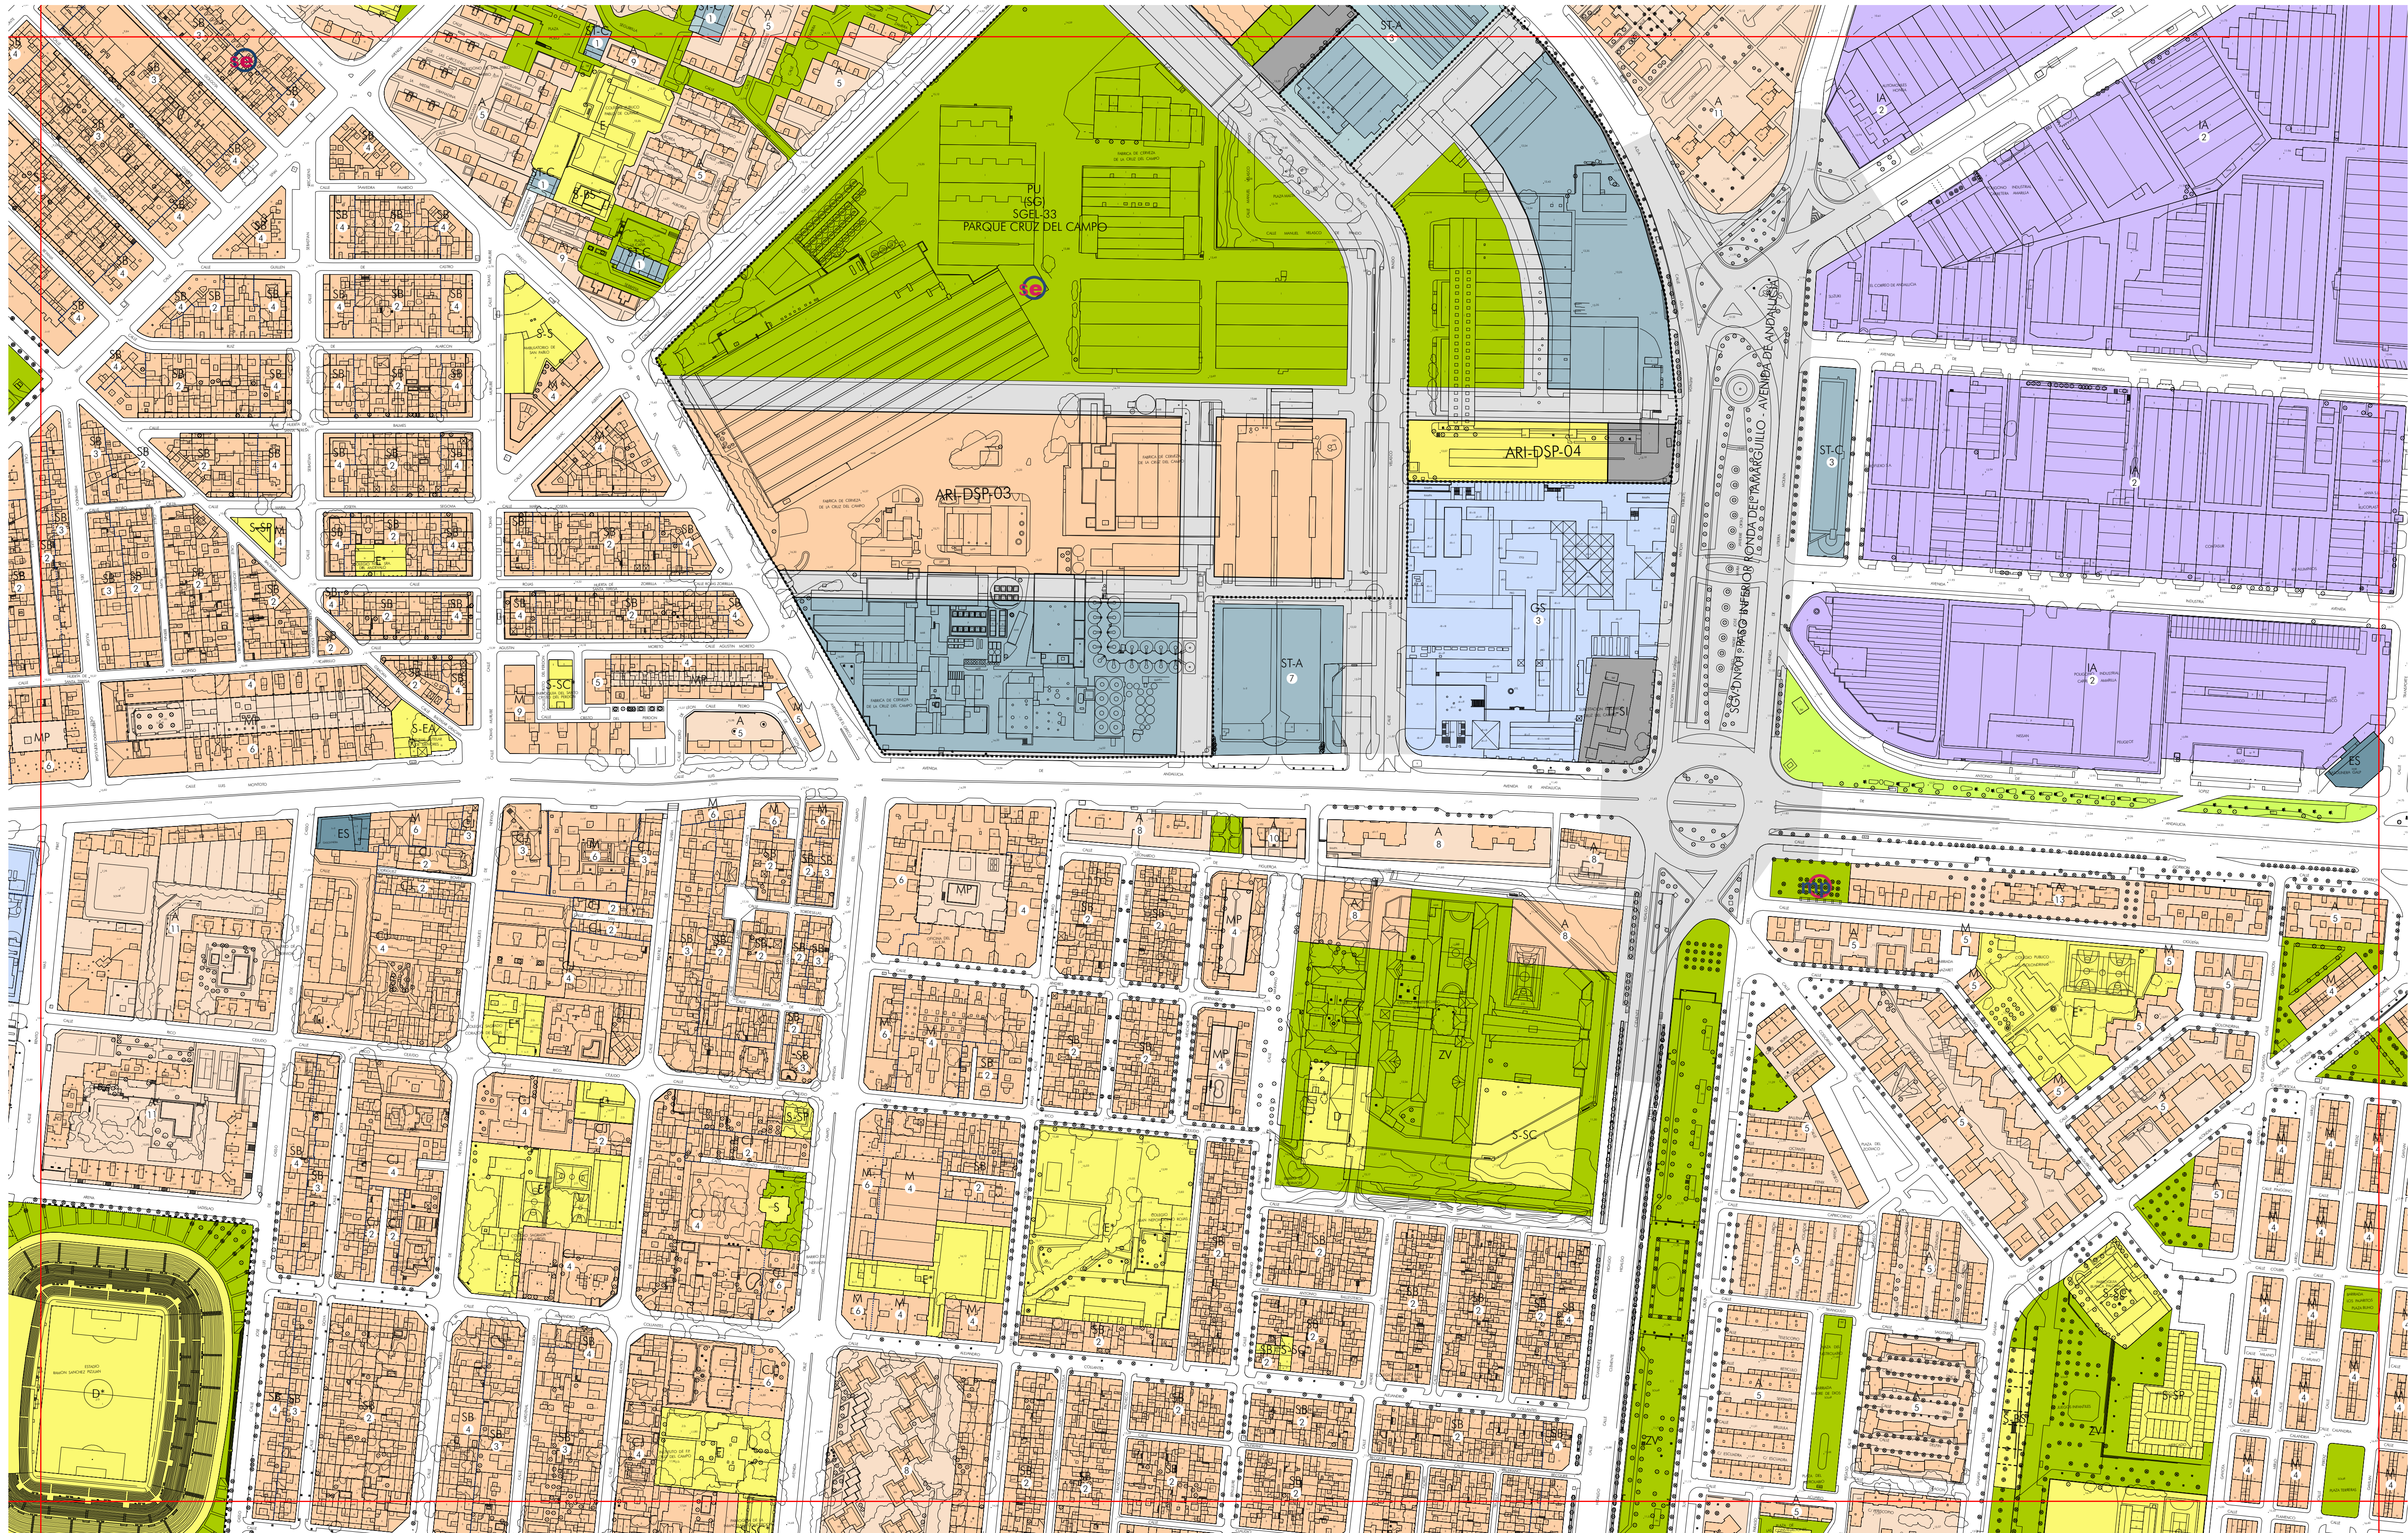

USOS GLOBALES Y PORMENORIZADOS

RESIDENCIAL

VIVIENDA



TERCIARIO

SERVICIOS



ACTIVIDADES PRODUCTIVAS

SERVICIOS



GRAN SUPERFICIE
COMERCIAL




INDUSTRIA Y ALMACENAMIENTO



DOTACIONAL

EQUIPAMIENTOS Y SERVICIOS PÚBLICOS

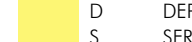

ESPACIOS LIBRES

PM




TRANSPORTES E INFRAESTRUCTURAS BÁSICAS

TI-SI



S

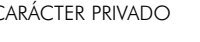

TI-F



TI-P



TI-AP



TI-HP



TI-T


S-S



S-SB



S-EA

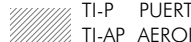

S-SC



S-SP



S-EES

ZONAS DE ORDENANZAS DEL SUELO URBANO

CH

CENTRO HISTÓRICO



M

EDIFICACIÓN EN MANZANA



MP

EDIFICACIÓN EN MANZANA



A

EDIFICACIÓN ABIERTA



SB

SUBURBANA



CA

CUIDAD JARDÍN

AD

UNIFAMILIAR ADOSADA



UA

UNIFAMILIAR AISLADA Y/O AGRUPADA

CT

CONSERVACIÓN TIPOLOGICA



IA

INDUSTRIA SINGULAR



IS

INDUSTRIA EN EDIFICACIÓN ABIERTA



IC

INDUSTRIA EN EDIFICACIÓN COMPACTA

SA

SERVICIOS AVANZADOS



ST-A

SERVICIOS TERCIARIOS EN EDIFICACIÓN ABIERTA



ST-C

SERVICIOS TERCIARIOS EN EDIFICACIÓN COMPACTA



CLASIFICACIÓN Y CATEGORÍAS DE SUELO. DETERMINACIONES COMPLEMENTARIAS

LÍMITE DEL TÉRMINO MUNICIPAL



DELIMITACIÓN DE SUELO URBANO




DELIMITACIÓN DE SECTORES, ÁREAS DE REFORMA INTERIOR, ÁREAS DE TRANSFERENCIA DE APROVECHAMIENTO, ACTUACIONES SIMPLES Y ÁREAS DE PLANEAMIENTO INCORPORADO



DELIMITACIÓN DE SUELO URBANIZABLE



SUELO URBANIZABLE ORDENADO

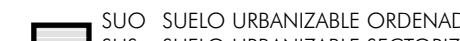

SUELO URBANIZABLE SECTORIZADO



SUELO URBANIZABLE NO SECTORIZADO

DOMINIO PÚBLICO MARÍTIMO TERRESTRE



LÍMITE ZONA DE SERVIDUMBRE DE PROTECCIÓN



LÍMITE ZONA DE SERVIDUMBRE DE PROTECCIÓN EN CONJUNTO HISTÓRICO



DOMINIO PÚBLICO MARÍTIMO TERRESTRE PROBABLE



LÍMITE ZONA DE SERVIDUMBRE DE PROTECCIÓN PROBABLE



LÍMITE ZONA DE SERVIDUMBRE DE PROTECCIÓN PROBABLE EN CONJUNTO HISTÓRICO



ALINEACIÓN EXTERIOR

ALINEACIÓN INTERIOR Y/O RETRANQUEOS OBLIGATORIOS

FONDO MÁXIMO EDIFICABLE Y PASAJE EN PLANTA BAJA

CAMBIO DE ALTURA Y/O ZONA DE ORDENANZA

ALTURA MÁXIMA

CONSERVACIÓN DE USO EXISTENTE

SISTEMA GENERAL

MURALLA. RESTOS EMERGENTES

13-13	14-13	15-13
13-14	14-14	15-14
13-15	14-15	15-15

ORDENACIÓN PORMENORIZADA COMPLETA

escala 1/2.000

OPS

gerencia de urbanismo EXCMO. AYUNTAMIENTO / NUEVO PLAN GENERAL DE ORDENACIÓN URBANÍSTICA. SEVILLA