


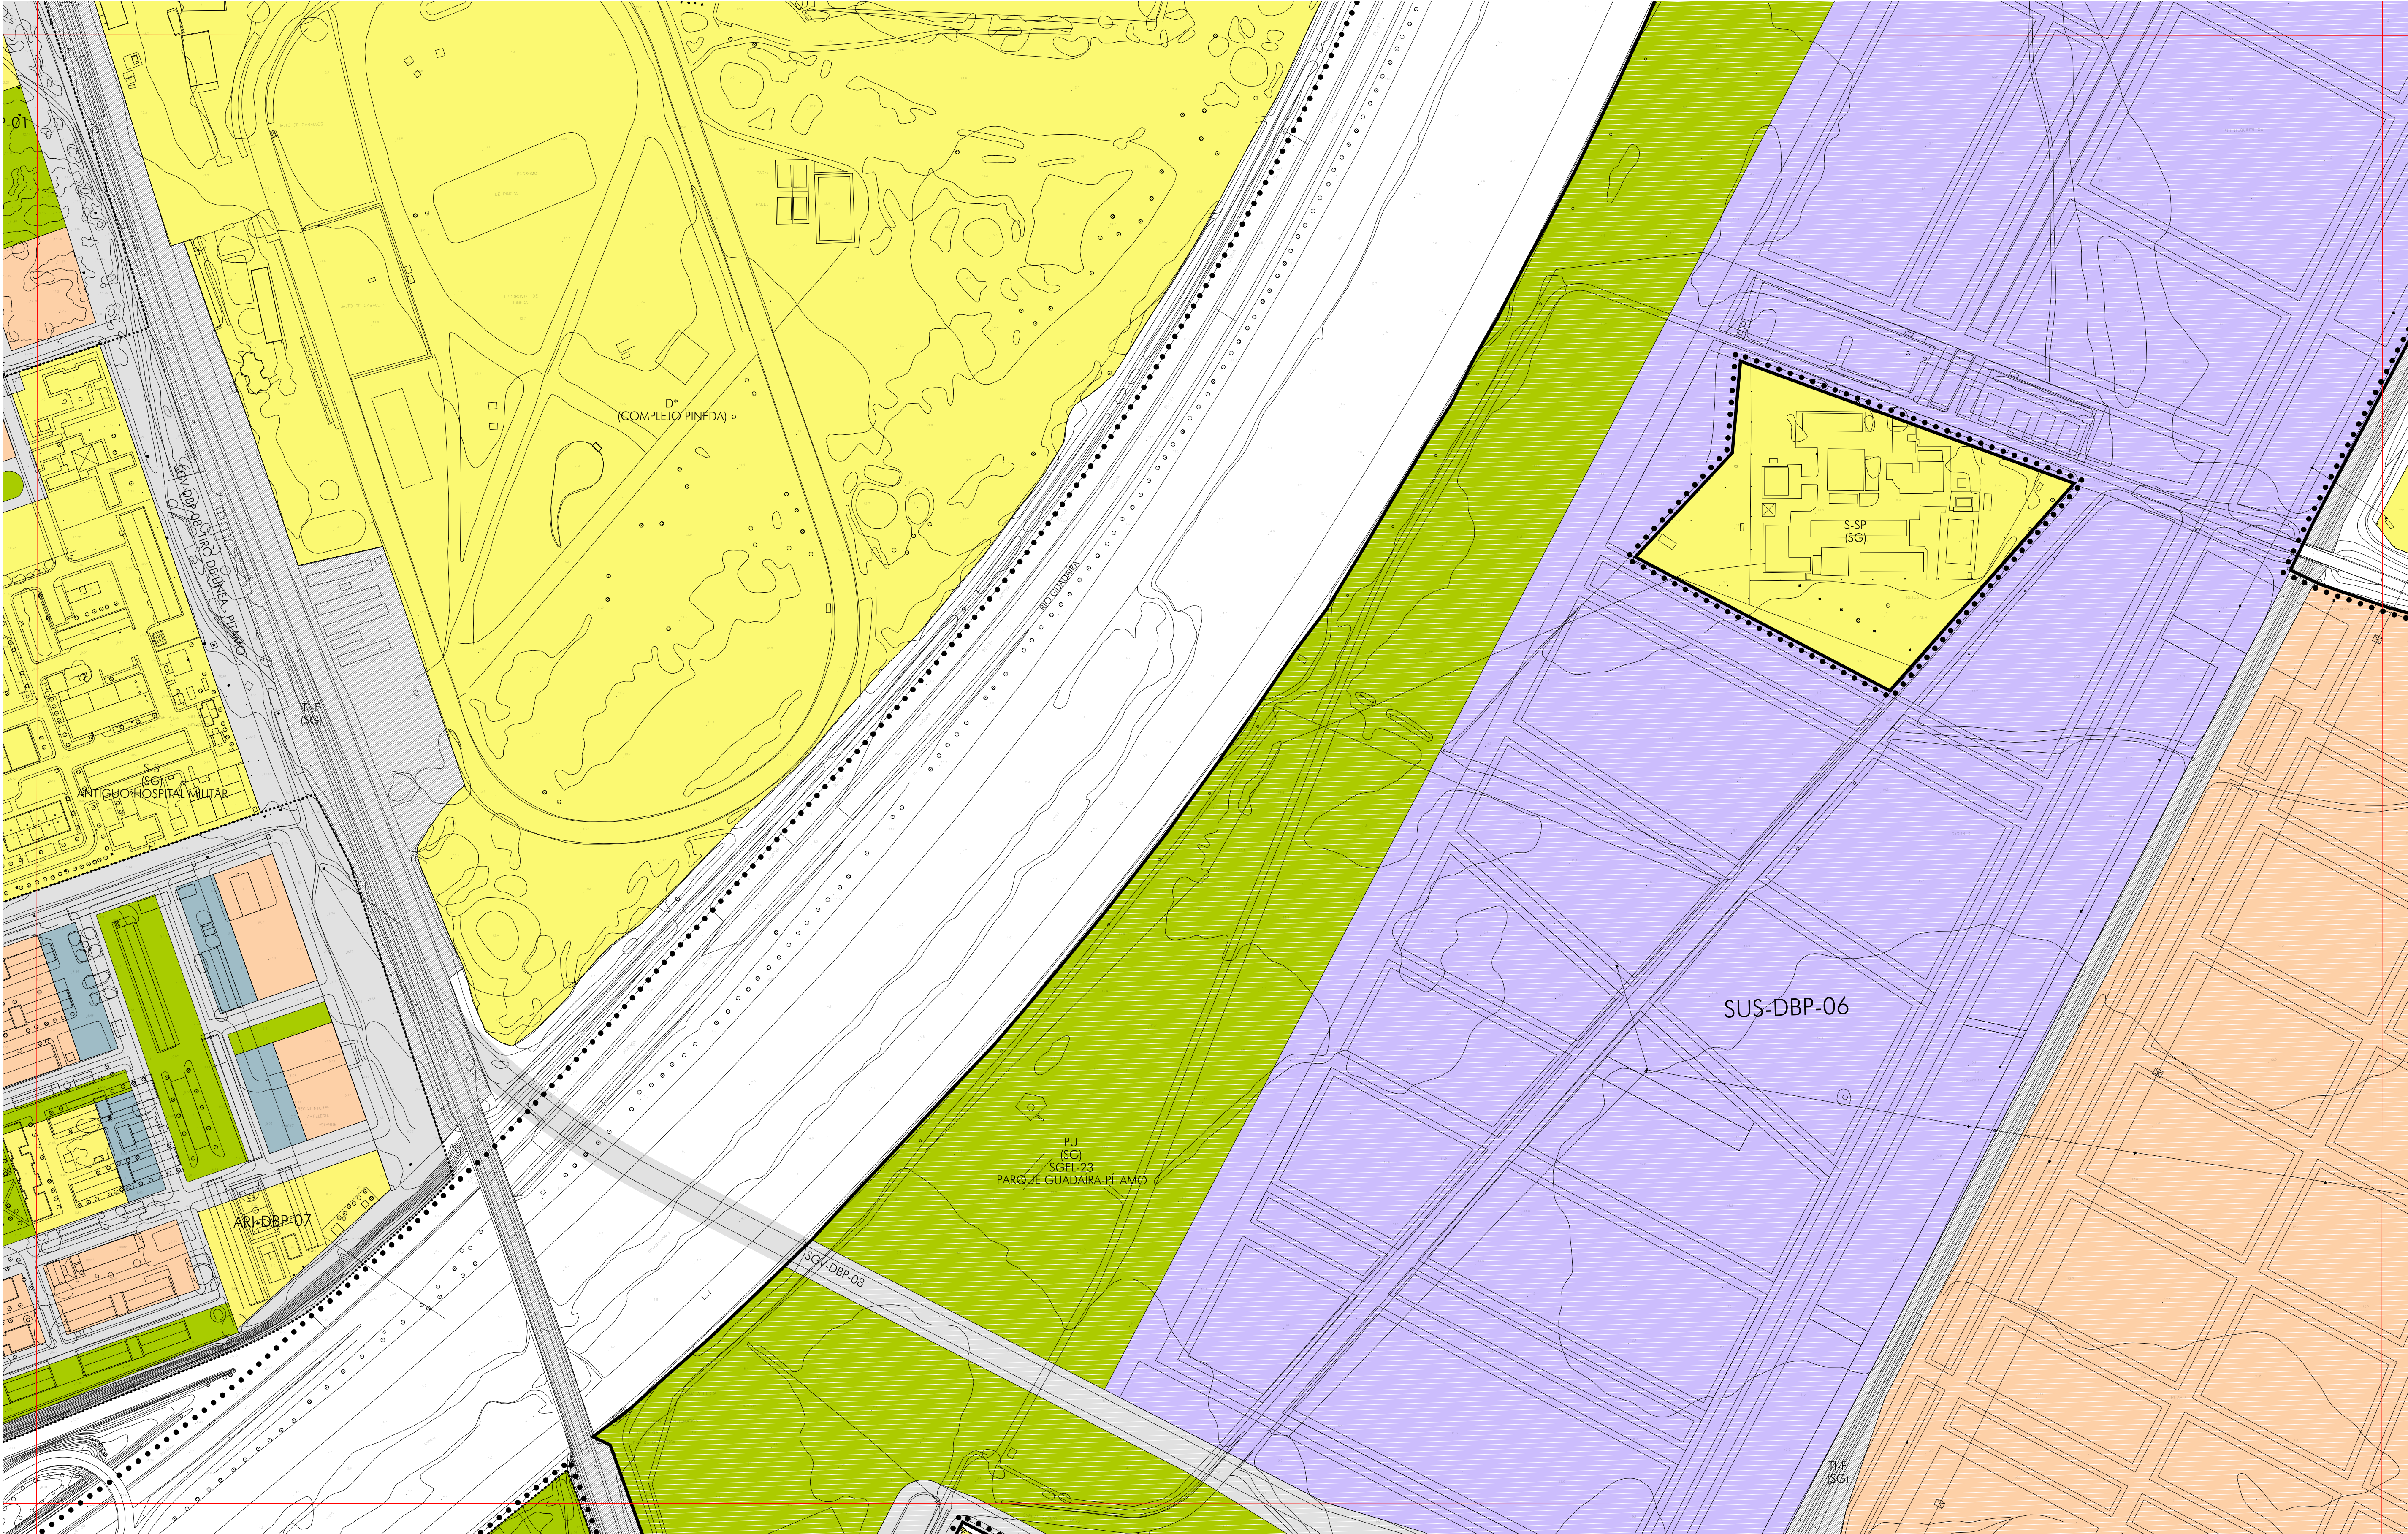

USOS GLOBALES Y PORMENORIZADOS

RESIDENCIAL

VIVIENDA

TERCIARIO
SERVICIOS TERCARIOS

GRAN SUPERFICIE COMERCIAL

ESTACIÓN DE SERVICIO

ACTIVIDADES PRODUCTIVAS
SERVICIOS AVANZADOS

INDUSTRIA Y ALMACENAMIENTO

DOTACIONAL

EQUIPAMIENTOS Y SERVICIOS PÚBLICOS

E EDUCATIVO
D DEPORTIVO
S SERVICIOS DE INTERÉS PÚBLICO Y SOCIAL DE CARÁCTER PRIVADO

ESPACIOS LIBRES

PM PARQUE METROPOLITANO
PU PARQUE URBANO
ZV ZONAS VERDES

TRANSPORTES E INFRAESTRUCTURAS BÁSICAS

TI-SI SERVICIOS INFRAESTRUCTURALES
TI-CTM CENTRO DE TRANSPORTE DE MERCANCÍAS

VIARIO PROPUESTO

ESPACIO LIBRE ASOCIADO AL VIARIO

S-S SERVICIOS DE INTERÉS PÚBLICO Y SOCIAL DE CARÁCTER PRIVADO
S-BS
S-EA
S-SC
S-SP
S-EES

TI-F FERROVIARIO
TI-P PUERTO
TI-AP AEROPUERTO
TI-HP HELIPUERTO
TI-IT INTERCAMBIADOR DE TRANSPORTE

ZONAS DE ORDENANZAS DEL SUELO URBANO

CH CENTRO HISTÓRICO
MA EDIFICACIÓN EN MANZANA
MP EDIFICACIÓN EN MANZANA CON ALINEACIÓN INTERIOR OBLIGATORIA O MÁXIMA
A EDIFICACIÓN ABIERTA
SB SUBURBANA
CJ CIUDAD JARDÍN
AD UNIFAMILIAR ADOSADA
UA UNIFAMILIAR AISLADA Y/O AGRUPADA
CT CONSERVACIÓN TIPOLOGICA
IS INDUSTRIA SINGULAR
IA INDUSTRIA EN EDIFICACIÓN ABIERTA
IC INDUSTRIA EN EDIFICACIÓN COMPACTA
SA SERVICIOS AVANZADOS
STA SERVICIOS TERCARIOS EN EDIFICACIÓN ABIERTA
ST-C SERVICIOS TERCARIOS EN EDIFICACIÓN COMPACTA

CLASIFICACIÓN Y CATEGORÍAS DE SUELO. DETERMINACIONES COMPLEMENTARIAS

— LÍMITE DEL TÉRMINO MUNICIPAL

..... DELIMITACIÓN DE SUELO URBANO

DELIMITACIÓN DE SECTORES, ÁREAS DE REFORMA INTERIOR, ÁREAS DE TRANSFERENCIA DE APROVECHAMIENTO, ACTUACIONES SIMPLES Y ÁREAS DE PLANEAMIENTO INCORPORADO

SOU SECTOR DE SUELO URBANO
ARI ÁREA DE REFORMA INTERIOR
ATA ÁREA DE TRANSFERENCIA DE APROVECHAMIENTO
AS ACTUACIÓN SIMPLE DE VIAJO, EQUIPAMIENTO O ESPACIOS LIBRES
API ÁREA DE PLANEAMIENTO INCORPORADO

DELIMITACIÓN DE SUELO URBANIZABLE

SUO SUELO URBANIZABLE ORDENADO
SUS SUELO URBANIZABLE SECTORIZADO
SUNS SUELO URBANIZABLE NO SECTORIZADO

DOMINIO PÚBLICO MARITIMO TERRESTRE

LÍMITE ZONA DE SERVIDUMBRE DE PROTECCIÓN

LÍMITE ZONA DE SERVIDUMBRE DE PROTECCIÓN EN CONJUNTO HISTÓRICO

DOMINIO PÚBLICO MARITIMO TERRESTRE PROBABLE

LÍMITE ZONA DE SERVIDUMBRE DE PROTECCIÓN PROBABLE

LÍMITE ZONA DE SERVIDUMBRE DE PROTECCIÓN PROBABLE EN CONJUNTO HISTÓRICO

ALINEACIÓN EXTERIOR

ALINEACIÓN INTERIOR Y/O RETRANQUEOS OBLIGATORIOS

FONDO MÁXIMO EDIFICABLE Y PASAJE EN PLANTA BAJA

CAMBIO DE ALTURA Y/O ZONA DE ORDENANZA

ALTURA MÁXIMA

CONSERVACIÓN DE USO EXISTENTE

SISTEMA GENERAL

MURALLA: RESTOS EMERGENTES

13-18	14-18	15-18
13-19	14-19	15-19
13-20	14-20	15-20

ORDENACIÓN PORMENORIZADA COMPLETA

escala 1/2.000

OPS
OFICINA DEL PLAN DE SEVILLA

gerencia de urbanismo EXCMO. AYUNTAMIENTO / NUEVO PLAN GENERAL DE ORDENACIÓN URBANÍSTICA SEVILLA