


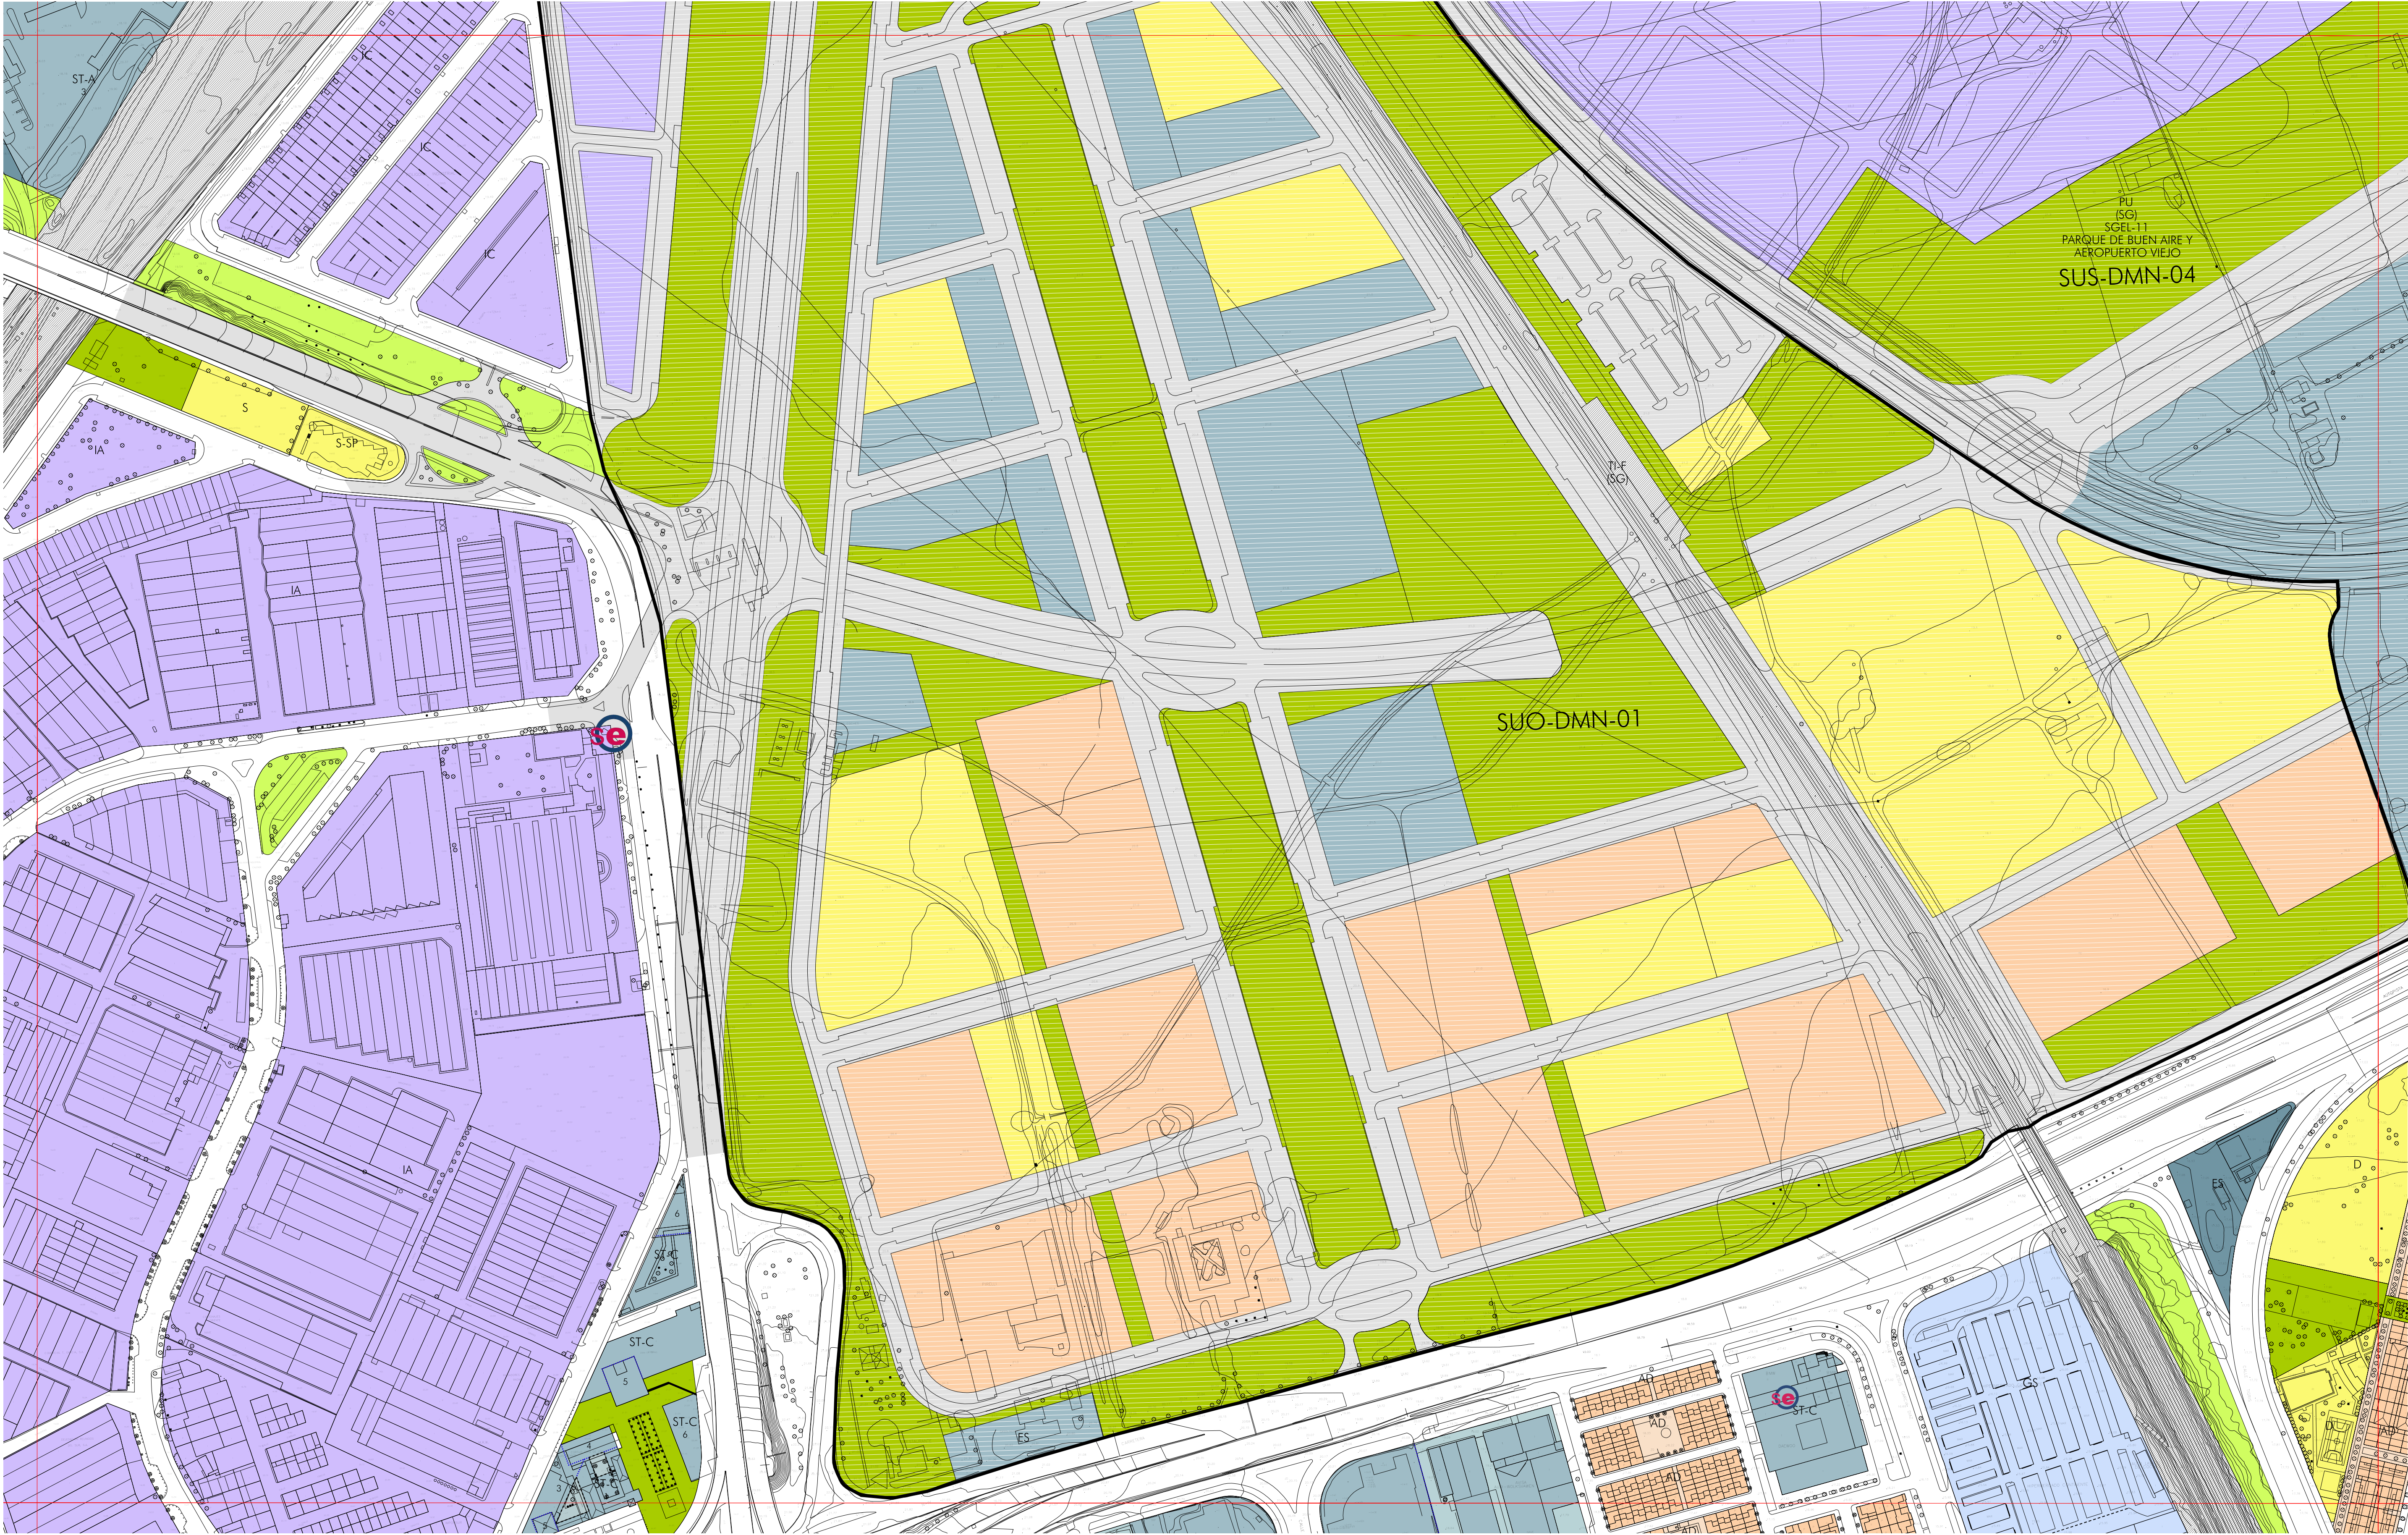

USOS GLOBALES Y PORMENORIZADOS

RESIDENCIAL

VIVIENDA




TERCIARIO

SERVICIOS

COMERCIAL

ESTACIÓN

DE SERVICIO

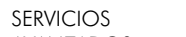

ACTIVIDADES PRODUCTIVAS

SERVICIOS

AVANZADOS

INDUSTRIA Y ALMACENAMIENTO

DOTACIONAL

EQUIPAMIENTOS Y SERVICIOS PÚBLICOS

E EDUCATIVO

D DEPORTIVO

S SERVICIOS DE INTERÉS PÚBLICO Y SOCIAL

(*) DE CARÁCTER PRIVADO

ESPACIOS LIBRES

PU PARQUE METROPOLITANO

PJ PARQUE URBANO

ZV ZONAS VERDES

TRANSPORTES E INFRAESTRUCTURAS BÁSICAS

TI-SI SERVICIOS

TI-AP INFRAESTRUCTURAS

TI-CTM CENTRO DE TRANSPORTE

DE MERCANCÍAS

VIARIO PROPUESTO

ESPACIO LIBRE ASOCIADO AL VIARIO

TI-F FERROVIARIO

TI-P PUERTO

TI-AP AEROPUERTO

TI-HF HELIPUERTO

TI-IT INTERCAMBIADOR

DE TRANSPORTE

ZONAS DE ORDENANZAS DEL SUELO URBANO

CH

CENTRO HISTÓRICO

M

EDIFICACIÓN EN MANZANA

MP

EDIFICACIÓN EN MANZANA

A

CON ALINEACIÓN INTERIOR OBLIGATORIA O MÁXIMA

SB

EDIFICACIÓN ABIERTA

SB

SUBURBANA

CJ

CUIDAD JARDÍN

AD

UNIFAMILIAR ADOSADA

UA

UNIFAMILIAR AISLADA Y/O AGRUPADA

IC

CONSERVACIÓN TIPOLOGICA

IS

INDUSTRIA SINGULAR

IA

INDUSTRIA EN EDIFICACIÓN ABIERTA

IC

INDUSTRIA EN EDIFICACIÓN COMPACTA

SA

SERVICIOS AVANZADOS

ST-A

SERVICIOS TERCIARIOS EN EDIFICACIÓN ABIERTA

ST-C

SERVICIOS TERCIARIOS EN EDIFICACIÓN COMPACTA

CLASIFICACIÓN Y CATEGORÍAS DE SUELO. DETERMINACIONES COMPLEMENTARIAS

— LÍMITE DEL TÉRMINO MUNICIPAL

..... DELIMITACIÓN DE SUELO URBANO

DELIMITACIÓN DE SECTORES, ÁREAS DE REFORMA INTERIOR, ÁREAS DE TRANSFERENCIA DE APROVECHAMIENTO, ACTUACIONES SIMPLES Y ÁREAS DE PLANEAMIENTO INCORPORADO

SOU SECTOR DE SUELO URBANO

ARI ÁREA DE REFORMA INTERIOR

ATA ÁREA DE TRANSFERENCIA DE APROVECHAMIENTO

AS ACTUACIÓN SIMPLE DE VARIO, EQUIPAMIENTO O ESPACIOS LIBRES

API ÁREA DE PLANEAMIENTO INCORPORADO

DELIMITACIÓN DE SUELO URBANIZABLE

SUO SUELO URBANIZABLE ORDENADO

SUS SUELO URBANIZABLE SECTORIZADO

SUNS SUELO URBANIZABLE NO SECTORIZADO

DOMINIO PÚBLICO MARÍTIMO TERRESTRE

LÍMITE ZONA DE SERVIDUMBRE DE PROTECCIÓN

LÍMITE ZONA DE SERVIDUMBRE DE PROTECCIÓN EN CONJUNTO HISTÓRICO

DOMINIO PÚBLICO MARÍTIMO TERRESTRE PROBABLE

LÍMITE ZONA DE SERVIDUMBRE DE PROTECCIÓN PROBABLE

LÍMITE ZONA DE SERVIDUMBRE DE PROTECCIÓN PROBABLE EN CONJUNTO HISTÓRICO

ALINEACIÓN EXTERIOR

ALINEACIÓN INTERIOR Y/O RETRANQUEOS OBLIGATORIOS

FONDO MÁXIMO EDIFICABLE Y PASAJE EN PLANTA BAJA

CAMBIO DE ALTURA Y/O ZONA DE ORDENANZA

2 ALTURA MÁXIMA

CONSERVACIÓN DE USO EXISTENTE

SISTEMA GENERAL

MURALLA. RESTOS EMERGENTES

14-10	15-10	16-10
14-11	15-11	16-11
14-12	15-12	16-12

ORDENACIÓN

ORDENACIÓN PORMENORIZADA COMPLETA

escala 1/2.000

OPS

gerencia de urbanismo

EXCMO. AYUNTAMIENTO / NUEVO PLAN GENERAL DE ORDENACIÓN URBANÍSTICA. SEVILLA