


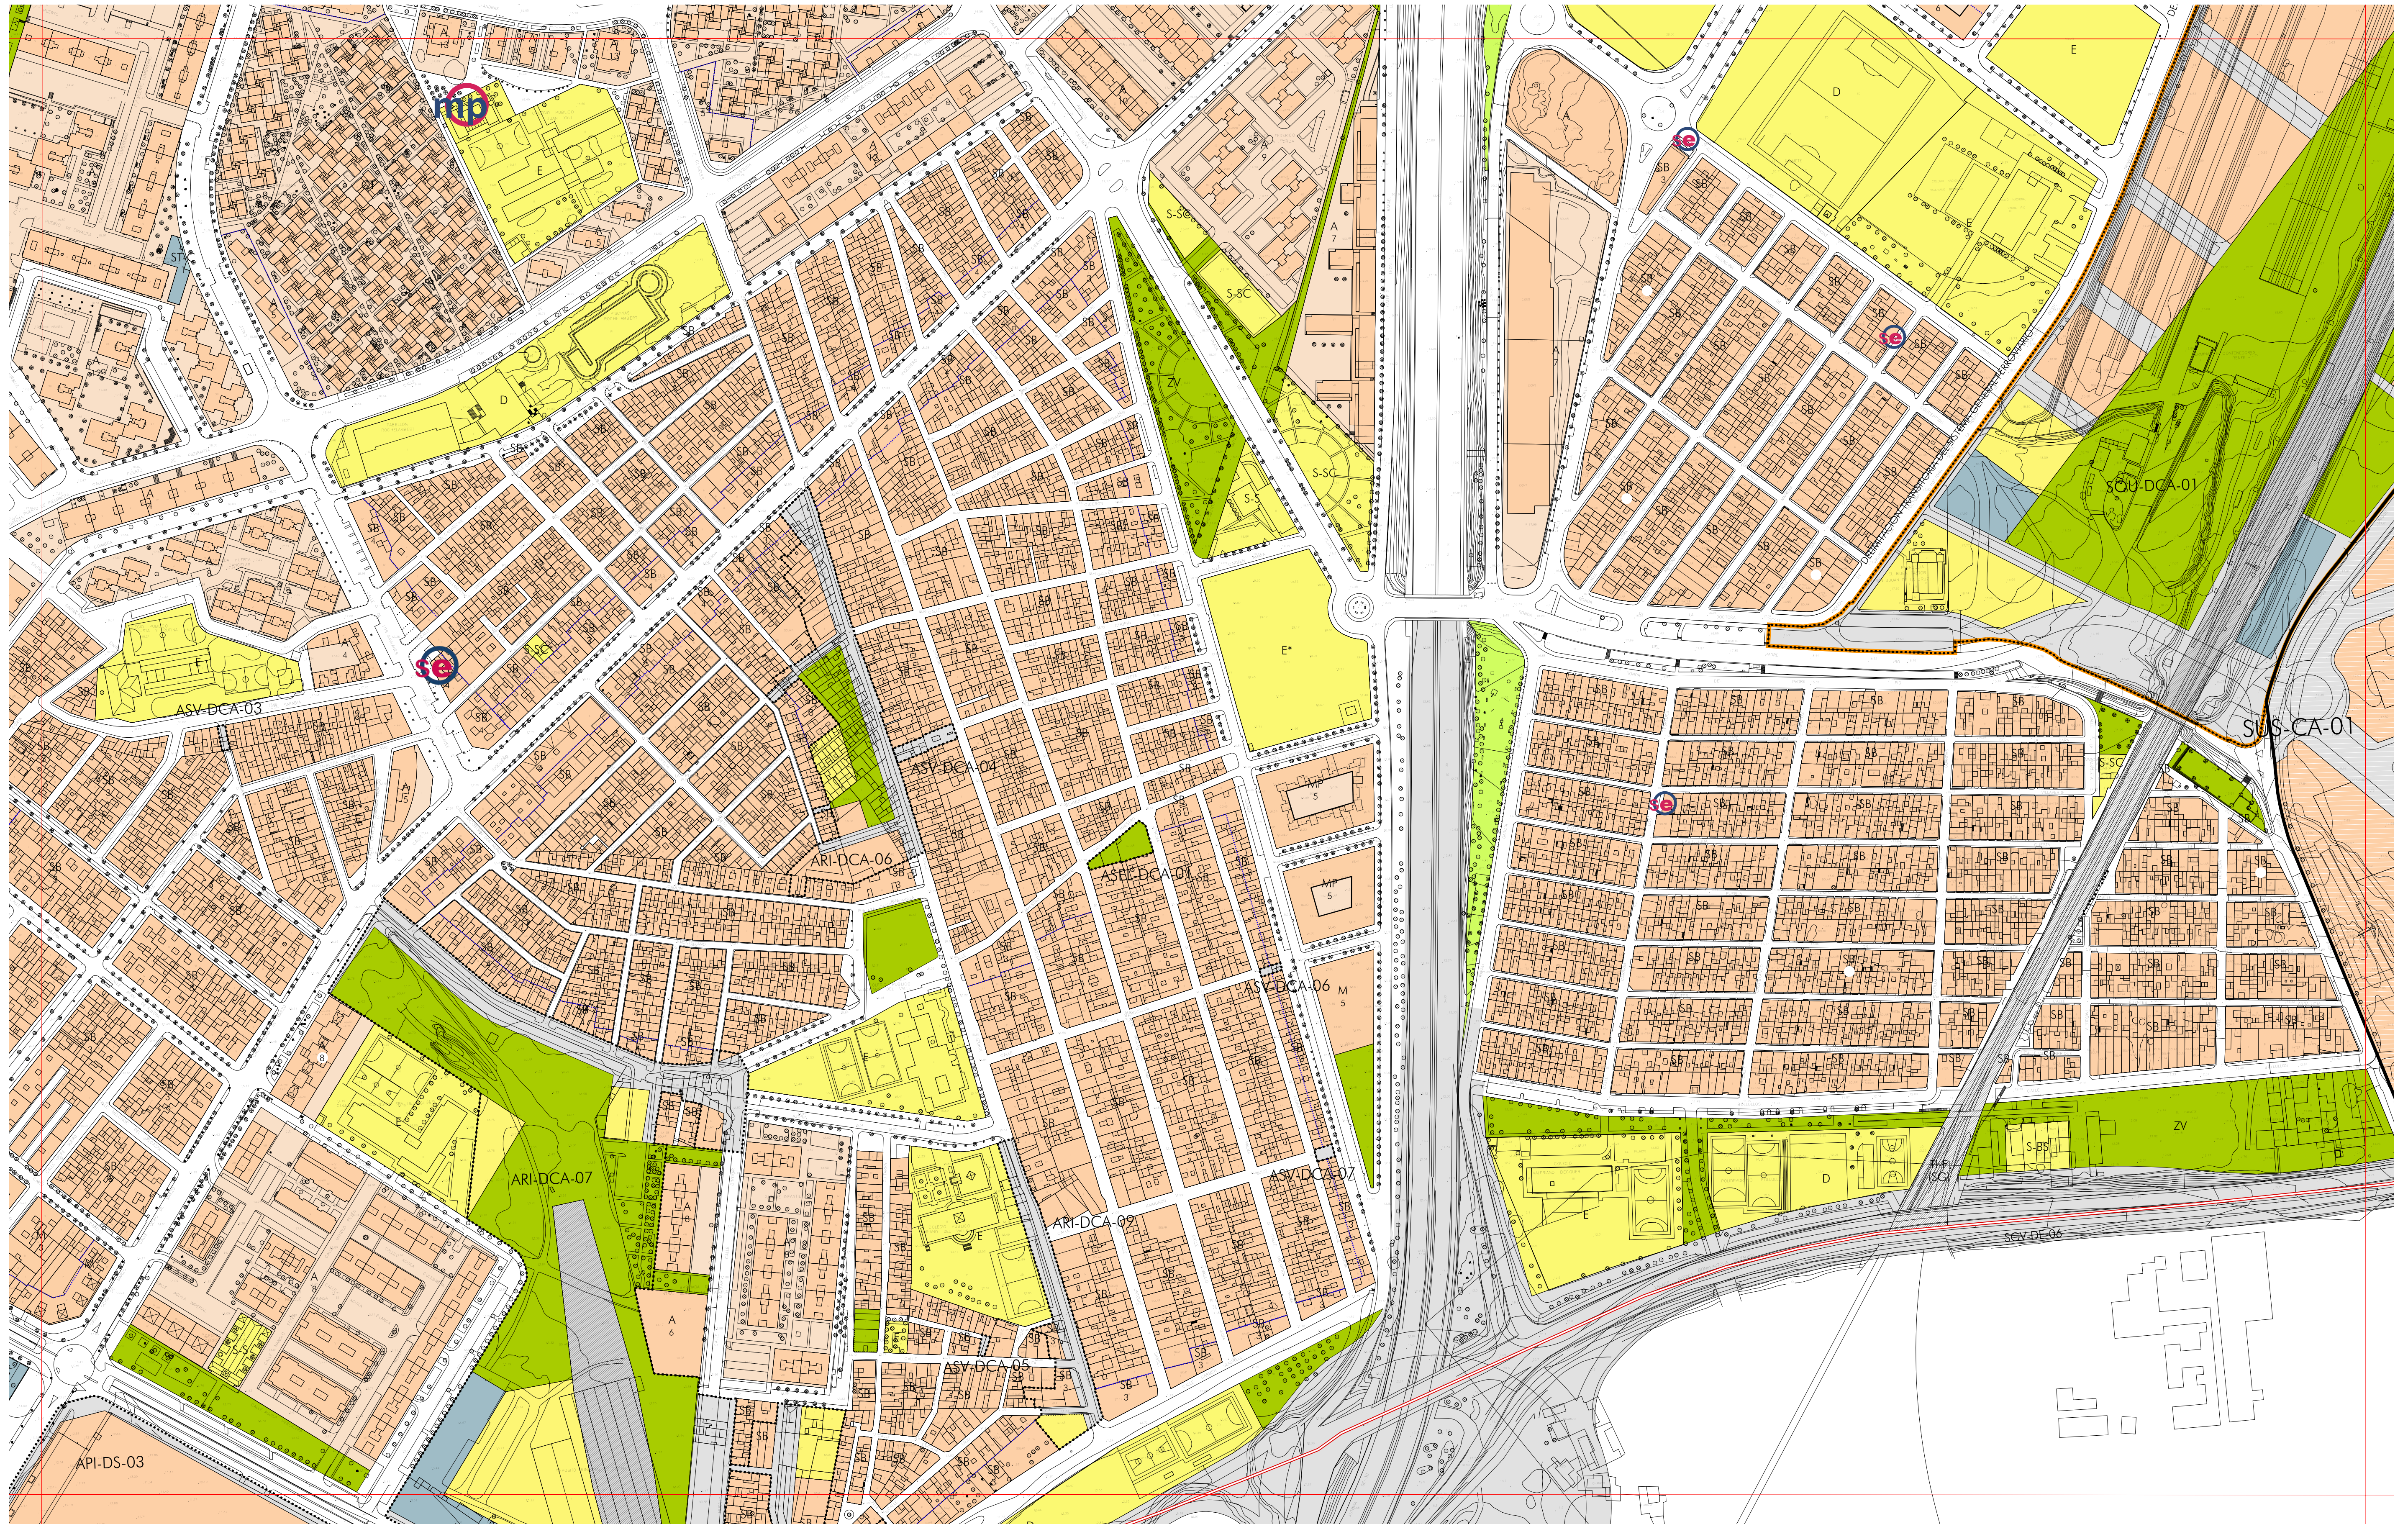

USOS GLOBALES Y PORMENORIZADOS

RESIDENCIAL

TERCIARIO

SERVICIOS
TERCIARIOS

GRAN SUPERFICIE
COMERCIAL

ESTACIÓN
DE SERVICIO

ACTIVIDADES PRODUCTIVAS

SERVICIOS
AVANZADOS

DOTACIONAL
EQUIPAMIENTOS Y SERVICIOS PÚBLICOS
E EDUCATIVO

D	DEPORTIVO	
S	SERVICIOS DE INTERÉS PÚBLICO Y SOCIAL	S-S
(*)	DE CARÁCTER PRIVADO	S-BS

ESPACIOS LIBRES

PM	PARQUE METROPOLITANO
PU	PARQUE URBANO

ZV	ZONAS VERDES	S-EES
TRANSPORTES E INFRAESTRUCTURAS BÁSICAS	TI-F	FERRO
TI-SI	SERVICIOS	TI-P
		PUERTO

TI-CTM	INFRAESTRUCTURALES CENTRO DE TRANSPORTE DE MERCANCÍAS	TI-AP	AEROPUERTO
		TI-HP	HELIPUERTO
		TI-IT	INTERCAMBIO DE TRÁFICO

ZONAS DE ORDENANZAS DEL SUELO URBANO

CH	CENTRO HISTÓRICO
ED	EDIFICACIÓN EN MANZANA
MP	EDIFICACIÓN EN MANZANA
	CON ALINEACIÓN INTERIOR OBLIGATORIA O MÁXIMA
A	EDIFICACIÓN ABIERTA
SB	SUBURBANA
CJ	CIUDAD JARDÍN
AD	UNIFAMILIAR ADOSADA
UA	UNIFAMILIAR AISLADA Y/O AGRUPADA
CT	CONSERVACIÓN TIPOLOGICA
IS	INDUSTRIA SINGULAR
IA	INDUSTRIA EN EDIFICACIÓN ABIERTA
IC	INDUSTRIA EN EDIFICACIÓN COMPACTA
SA	SERVICIOS AVANZADOS
ST-A	SERVICIOS TERCIARIOS EN EDIFICACIÓN ABIERTA
ST-C	SERVICIOS TERCIARIOS EN EDIFICACIÓN COMPACTA

CLASIFICACIÓN Y CATEGORÍAS DE SUELO. DETERMINACIONES COMPLEMENTARIAS

===== LÍMITE DEL TÉRMINO MUNICIPAL

● ● ● ● ● DELIMITACIÓN DE SUELO URBANO

DELIMITACIÓN DE SECTORES, ÁREAS DE REFORMA INTERIOR,
ÁREAS DE TRANSFERENCIA DE APROVECHAMIENTO, ACTUACIONES SIMPLES Y
ÁREAS DE PLANEAMIENTO INCORPORADO

 SOU SECTOR DE SUELO URBANO
 ARI ÁREA DE REFORMA INTERIOR
 ATA ÁREA DE TRANSFERENCIA DE APROVECHAMIENTO
 AS ACTUACIÓN SIMPLE DE VIARIO, EQUIPAMIENTO O ESPACIOS LIBRES
 API ÁREA DE PLANIFICAMIENTO INCORPORADO

DELIMITACIÓN DE SUELO URBANIZABLE

	SUO SUELO URBANIZABLE ORDENADO
SUS	SUELO URBANIZABLE SECTORIZADO
SUNS	SUELO URBANIZABLE NO SECTORIZADO

 DOMINIO PÚBLICO MARÍTIMO TERRESTRE
 LÍMITE ZONA DE SERVIDUMBRE DE PROTECCIÓN
 LÍMITE ZONA DE SERVIDUMBRE DE PROTECCIÓN EN CONJUNTO HISTÓRICO

 DOMINIO PÚBLICO MARÍTIMO TERRESTRE PROBABLE
    LÍMITE ZONA DE SERVIDUMBRE DE PROTECCIÓN PROBABLE
 LÍMITE ZONA DE SERVIDUMBRE DE PROTECCIÓN PROBABLE EN CONJUNTO H

— ALINEACIÓN EXTERIOR
— ALINEACIÓN INTERIOR Y/O RETRANQUEOS OBLIGATORIOS

----- FONDO MÁXIMO EDIFICABLE Y PASAJE EN PLANTA BAJA
..... CAMBIO DE ALTURA Y/O ZONA DE ORDENANZA

2	ALTURA MÁXIMA	14
▲	CONSERVACIÓN DE USO EXISTENTE	

(SG)	SISTEMA GENERAL	14
	MURALLA. RESTOS EMERGENTES	

ORDENACIÓN PORMENORIZADA COMPLETA

escala 1/2.000



gerencia de urbanismo EXCMO. AYUNTAMIENTO / NUEVO PLAN GENERAL DE ORDENACIÓN URBANÍSTICA. SEVILLA

14-15	15-15	16-15
14-16	15-16	16-16
14-17	15-17	