


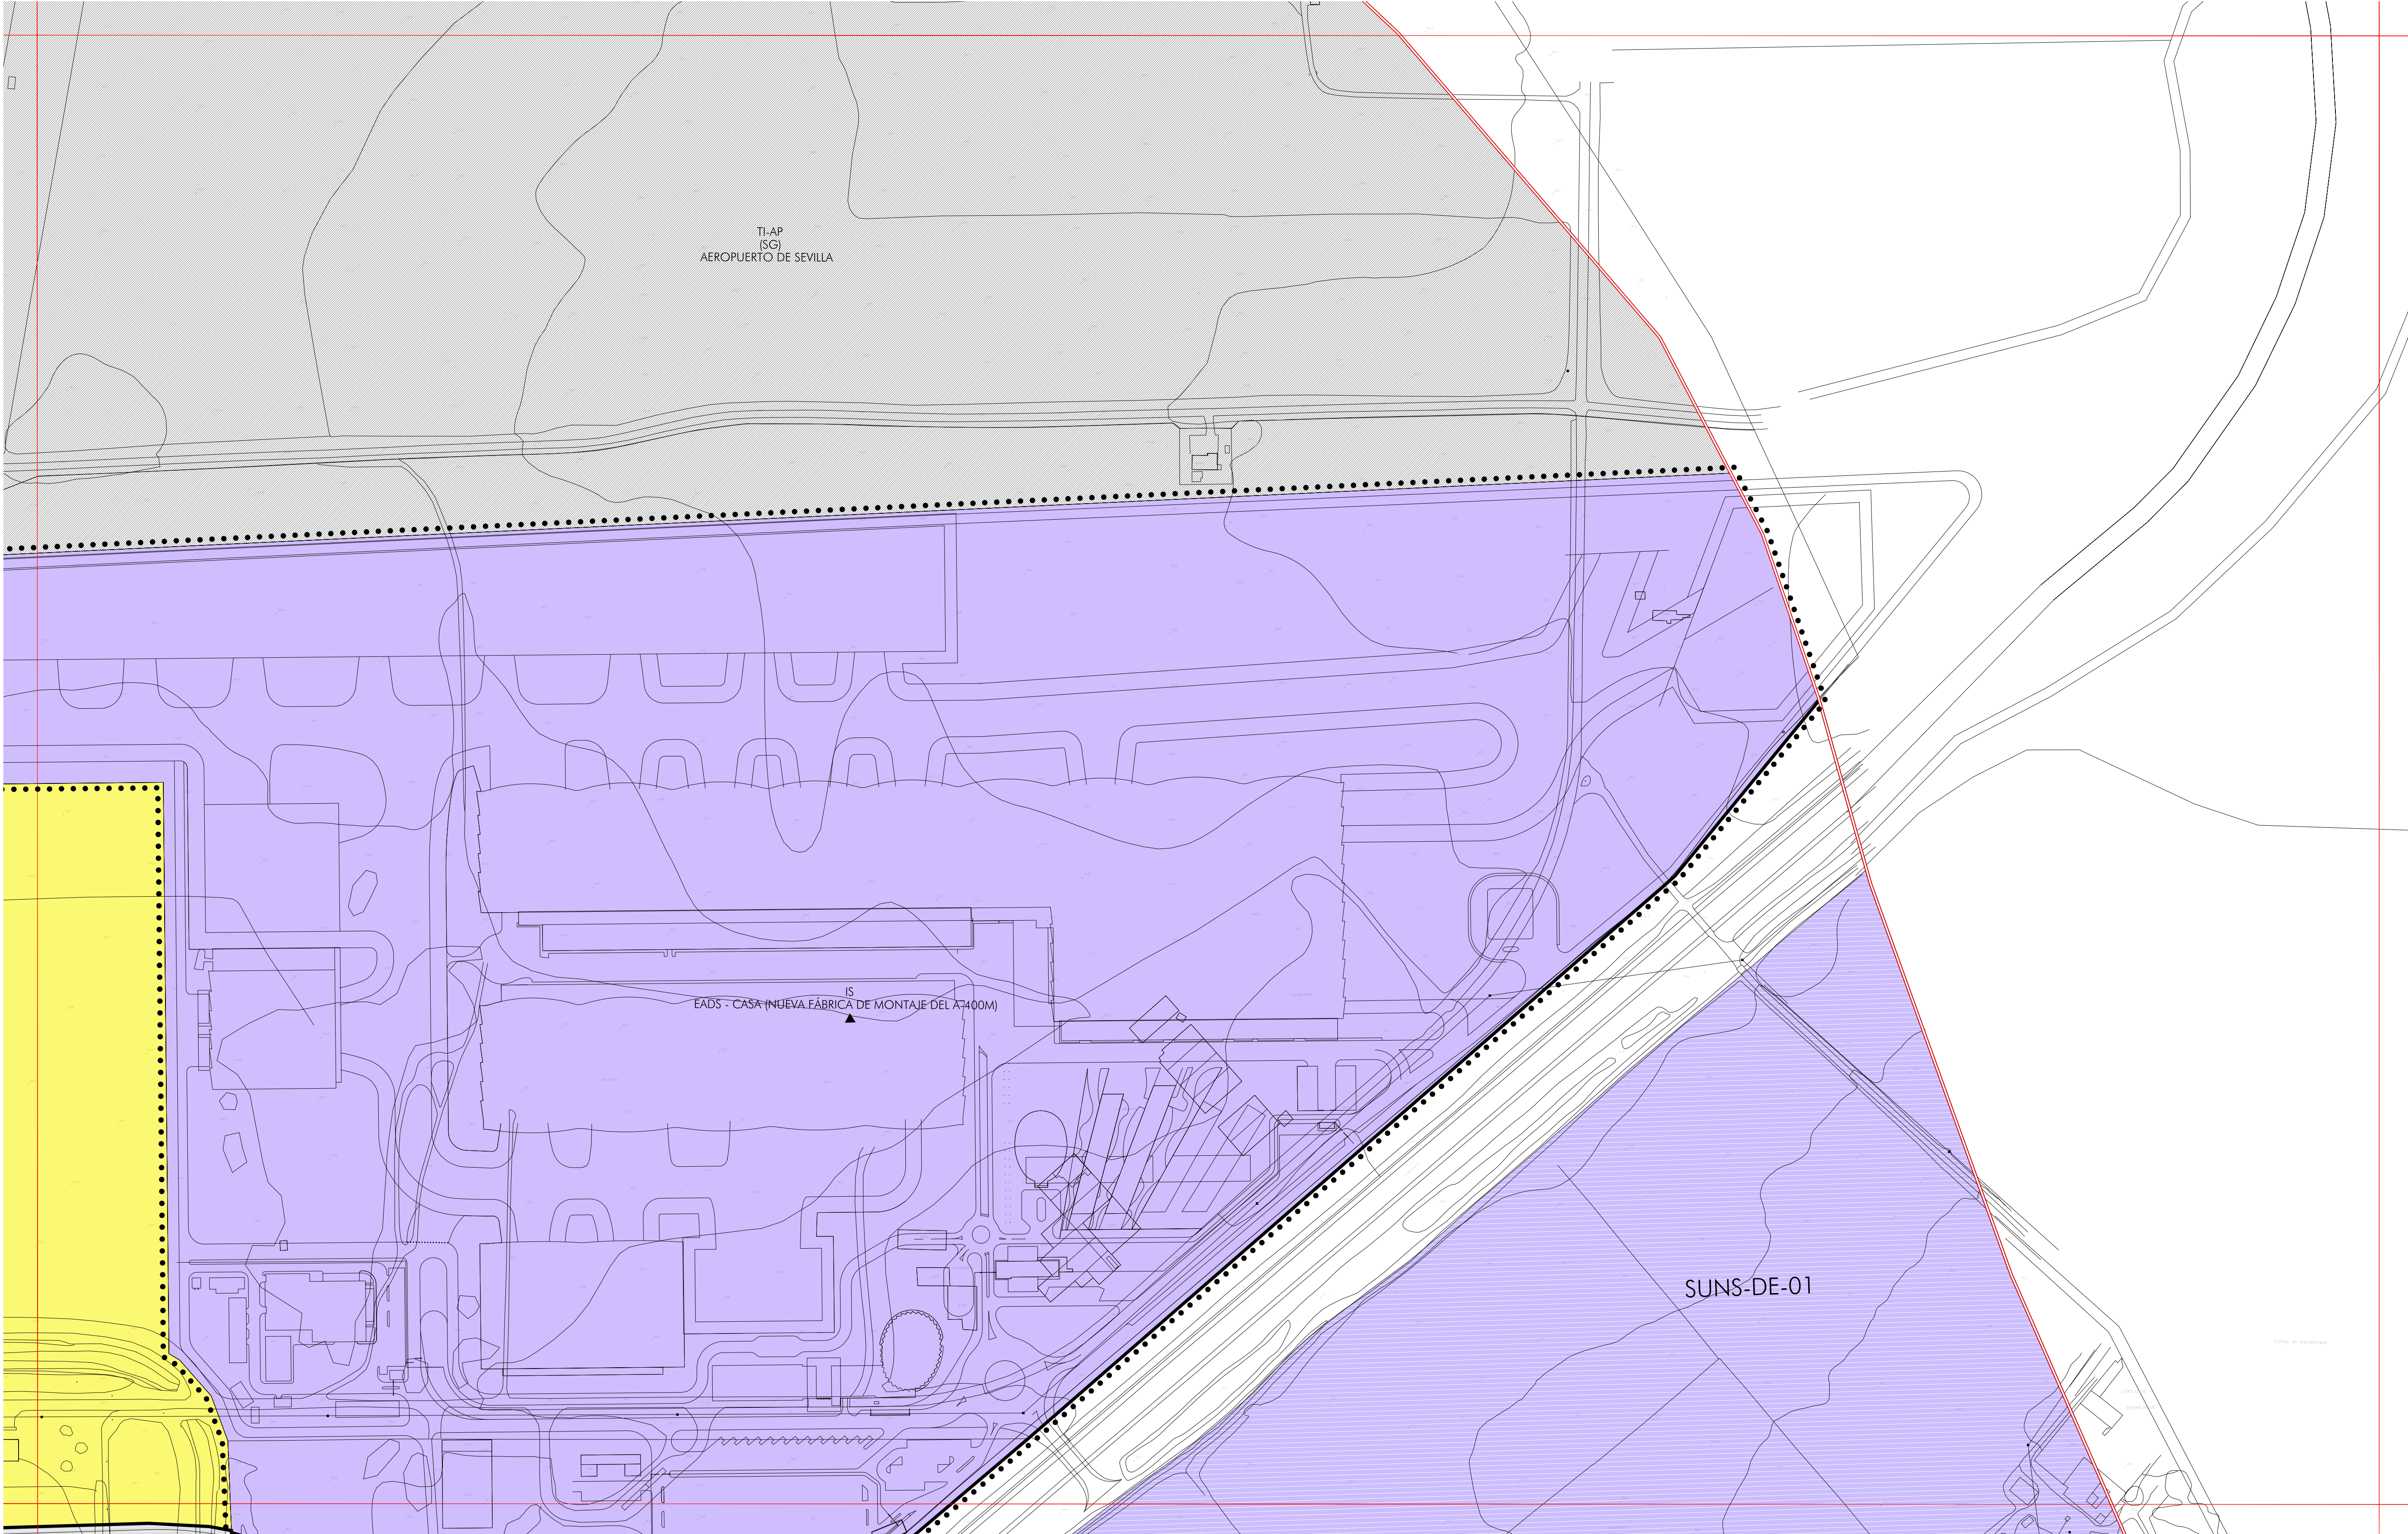

USOS GLOBALES Y PORMENORIZADOS

RESIDENCIAL

- VIVIENDA
- TERCIARIO
SERVICIOS
TERCARIOS
- GRAN SUPERFICIE
COMERCIAL
- ESTACIÓN
DE SERVICIO
- ACTIVIDADES PRODUCTIVAS
SERVICIOS
AVANZADOS
- INDUSTRIA Y ALMACENAMIENTO

DOTACIONAL

- EQUIPAMIENTOS Y SERVICIOS PÚBLICOS
- E EDUCATIVO
D DEPORTIVO
S SERVICIOS DE INTERÉS PÚBLICO Y SOCIAL
(*) DE CARÁCTER PRIVADO
- ESPACIOS LIBRES
- PM PARQUE METROPOLITANO
PU PARQUE URBANO
ZV ZONAS VERDES
- TRANSPORTES E INFRAESTRUCTURAS BÁSICAS
- TI-SI SERVICIOS
TI-PI INFRAESTRUCTURAS
TI-CTM CENTRO DE TRANSPORTE
DE MERCANCÍAS
- TI-F FERROVIARIO
TI-P PUERTO
TI-AP AEROPUERTO
TI-HP HELIPUERTO
TI-IT INTERCAMBIADOR
DE TRANSPORTE
- VIARIO PROPUESTO
- ESPACIO LIBRE ASOCIADO AL VIARIO

ZONAS DE ORDENANZAS DEL SUELO URBANO

- CH CENTRO HISTÓRICO
MA EDIFICACIÓN EN MANZANA
MP EDIFICACIÓN EN MANZANA
CON ALINEACIÓN INTERIOR OBLIGATORIA O MÁXIMA
A EDIFICACIÓN ABIERTA
SB SUBURBANA
CJ CIUDAD JARDÍN
AD UNIFAMILIAR ADOSADA
UA UNIFAMILIAR AISLADA Y/O AGRUPADA
CT CONSERVACIÓN TIPOLOGICA
IS INDUSTRIA SINGULAR
IA INDUSTRIA EN EDIFICACIÓN ABIERTA
IC INDUSTRIA EN EDIFICACIÓN COMPACTA
SA SERVICIOS AVANZADOS
ST-A SERVICIOS TERCARIOS EN EDIFICACIÓN ABIERTA
ST-C SERVICIOS TERCARIOS EN EDIFICACIÓN COMPACTA

CLASIFICACIÓN Y CATEGORÍAS DE SUELO. DETERMINACIONES COMPLEMENTARIAS

- LÍMITE DEL TÉRMINO MUNICIPAL
- DELIMITACIÓN DE SUELO URBANO
- DELIMITACIÓN DE SECTORES, ÁREAS DE REFORMA INTERIOR, ÁREAS DE TRANSFERENCIA DE APROVECHAMIENTO, ACTUACIONES SIMPLES Y ÁREAS DE PLANEAMIENTO INCORPORADO
- SOU SECTOR DE SUELO URBANO
ARI ÁREA DE REFORMA INTERIOR
ATA ÁREA DE TRANSFERENCIA DE APROVECHAMIENTO
AS ACTUACIÓN SIMPLE DE VIARIO, EQUIPAMIENTO O ESPACIOS LIBRES
API ÁREA DE PLANEAMIENTO INCORPORADO
- DELIMITACIÓN DE SUELO URBANIZABLE
- SUO SUELO URBANIZABLE ORDENADO
SUS SUELO URBANIZABLE SECTORIZADO
SUNS SUELO URBANIZABLE NO SECTORIZADO

- DOMINIO PÚBLICO MARÍTIMO TERRESTRE
LÍMITE ZONA DE SERVIDUMBRE DE PROTECCIÓN
LÍMITE ZONA DE SERVIDUMBRE DE PROTECCIÓN EN CONJUNTO HISTÓRICO
- DOMINIO PÚBLICO MARÍTIMO TERRESTRE PROBABLE
LÍMITE ZONA DE SERVIDUMBRE DE PROTECCIÓN PROBABLE
LÍMITE ZONA DE SERVIDUMBRE DE PROTECCIÓN PROBABLE EN CONJUNTO HISTÓRICO
- ALINEACIÓN EXTERIOR
ALINEACIÓN INTERIOR Y/O RETRANQUEOS OBLIGATORIOS
FONDO MÁXIMO EDIFICABLE Y PASAJE EN PLANTA BAJA
CAMBIO DE ALTURA Y/O ZONA DE ORDENANZA
- ② ALTURA MÁXIMA
CONSERVACIÓN DE USO EXISTENTE
SISTEMA GENERAL
MURALLA: RESTOS EMERGENTES

18-10	19-10	
18-11	19-11	
18-12	19-12	20-12

ORDENACIÓN

ORDENACIÓN PORMENORIZADA COMPLETA

escala 1/2.000

OPS
OFICINA DEL PLAN DE SEVILLA

gerencia de urbanismo EXCMO. AYUNTAMIENTO / NUEVO PLAN GENERAL DE ORDENACIÓN URBANÍSTICA SEVILLA